Zyra kadastrale komunale / Opštinska katastarska kancelarija: Ferizaj

Zona kadastrale / Katastarska zona: Talinoci i Jerlive

Lloji i njësisë kadastrale / Vrsta katastarske jedinice : Ndërtesë

Nr. i njësisë kadastrale / Br. katastarske jedinice : 00492-29

Numri i lëndës / Broj predmeta: _____

Shkalla e zvoglimit / Razmera plana 1: 500


Republika e Kosovës

Republika Kosova-Republic of Kosova

Qeveria -Vlada-Government

Ministria e Mjedisit dhe Planifikimit Hapësinor /Ministarstvo Sredine i Prostornog Planiranja/Ministry of Environment and Spatial Planning

AGJENCIA KADASTRALE E KOSOVËS/ KATASTARSKA AGECIJA KOSOVA/ KOSOVA CADASTRAL AGENCY

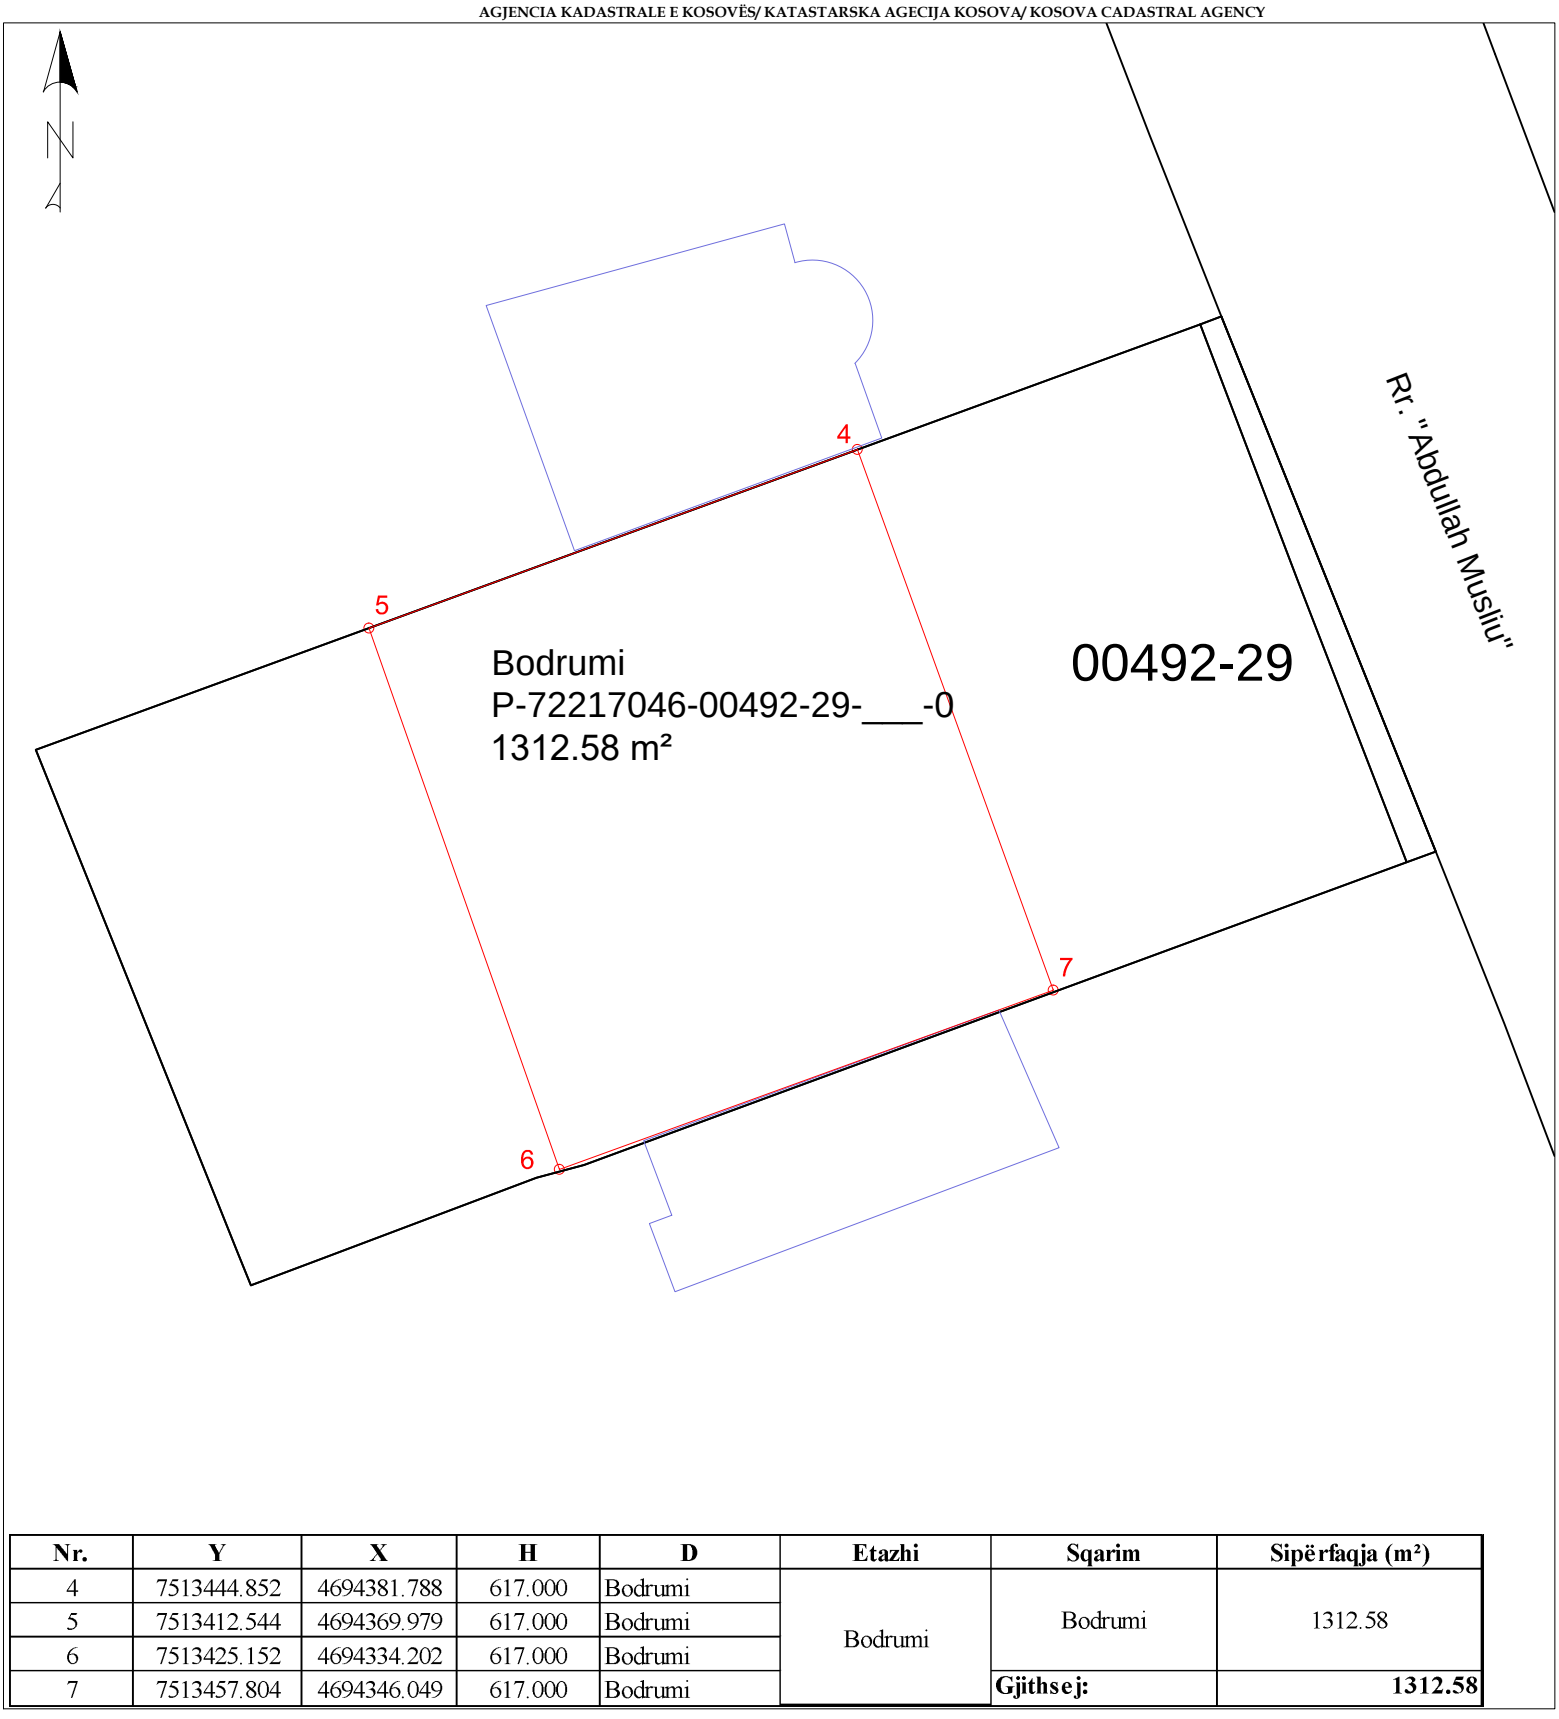

Nr.	Y	X	H	D	Etazhi	Sqarim	Sipërfaqja (m²)
4	7513444.852	4694381.788	617.000	Bodrumi	Bodrumi	Bodrumi	1312.58
5	7513412.544	4694369.979	617.000	Bodrumi			
6	7513425.152	4694334.202	617.000	Bodrumi			
7	7513457.804	4694346.049	617.000	Bodrumi		**Gjithsej:**	**1312.58**

Rilevoi / Snimio: LIRIDON SEJDIU

(emri dhe mbiemri i gjeodetit/kompanisë/ ime i prezime geodeta/ kompanije)

Nr. i licencës / Br. licence: 140

Nënshkrimi / Potpis: _____

Data e rilevimit / Datum snimanja: 13.08.2026

V.V.

Aprovoi / Usvojio: _____

(emri dhe mbiemri i përsonit zyrtar/ ime i prezime sluzbenog lica)

Nënshkrimi / Potpis: _____

Data e rilevimit / Datum snimanja: _____