Zyra kadastrale komunale / Opštinska katastarska kancelarija: Ferizaj

Nr. i njësisë kadastrale / Br. katastarske jedinice : 00492-29-___-0

Zona kadastrale / Katastarska zona: Talinoci i Jerlive

Numri i lëndës / Broj predmeta: _____

Lloji i njësisë kadastrale / Vrsta katastarske jedinice : Ndërtesë

Shkalla e zvoglimit / Razmera plana 1: 500


Republika e Kosovës

Republika Kosova-Republic of Kosova

Qeveria -Vlada-Government

Ministria e Mjedisit dhe Planifikimit Hapësinor /Ministarstvo Sredine i Prostornog Planiranja/Ministry of Environment and Spatial Planning

AGJENCIA KADASTRALE E KOSOVËS/ KATASTARSKA AGECIJA KOSOVA/ KOSOVA CADASTRAL AGENCY

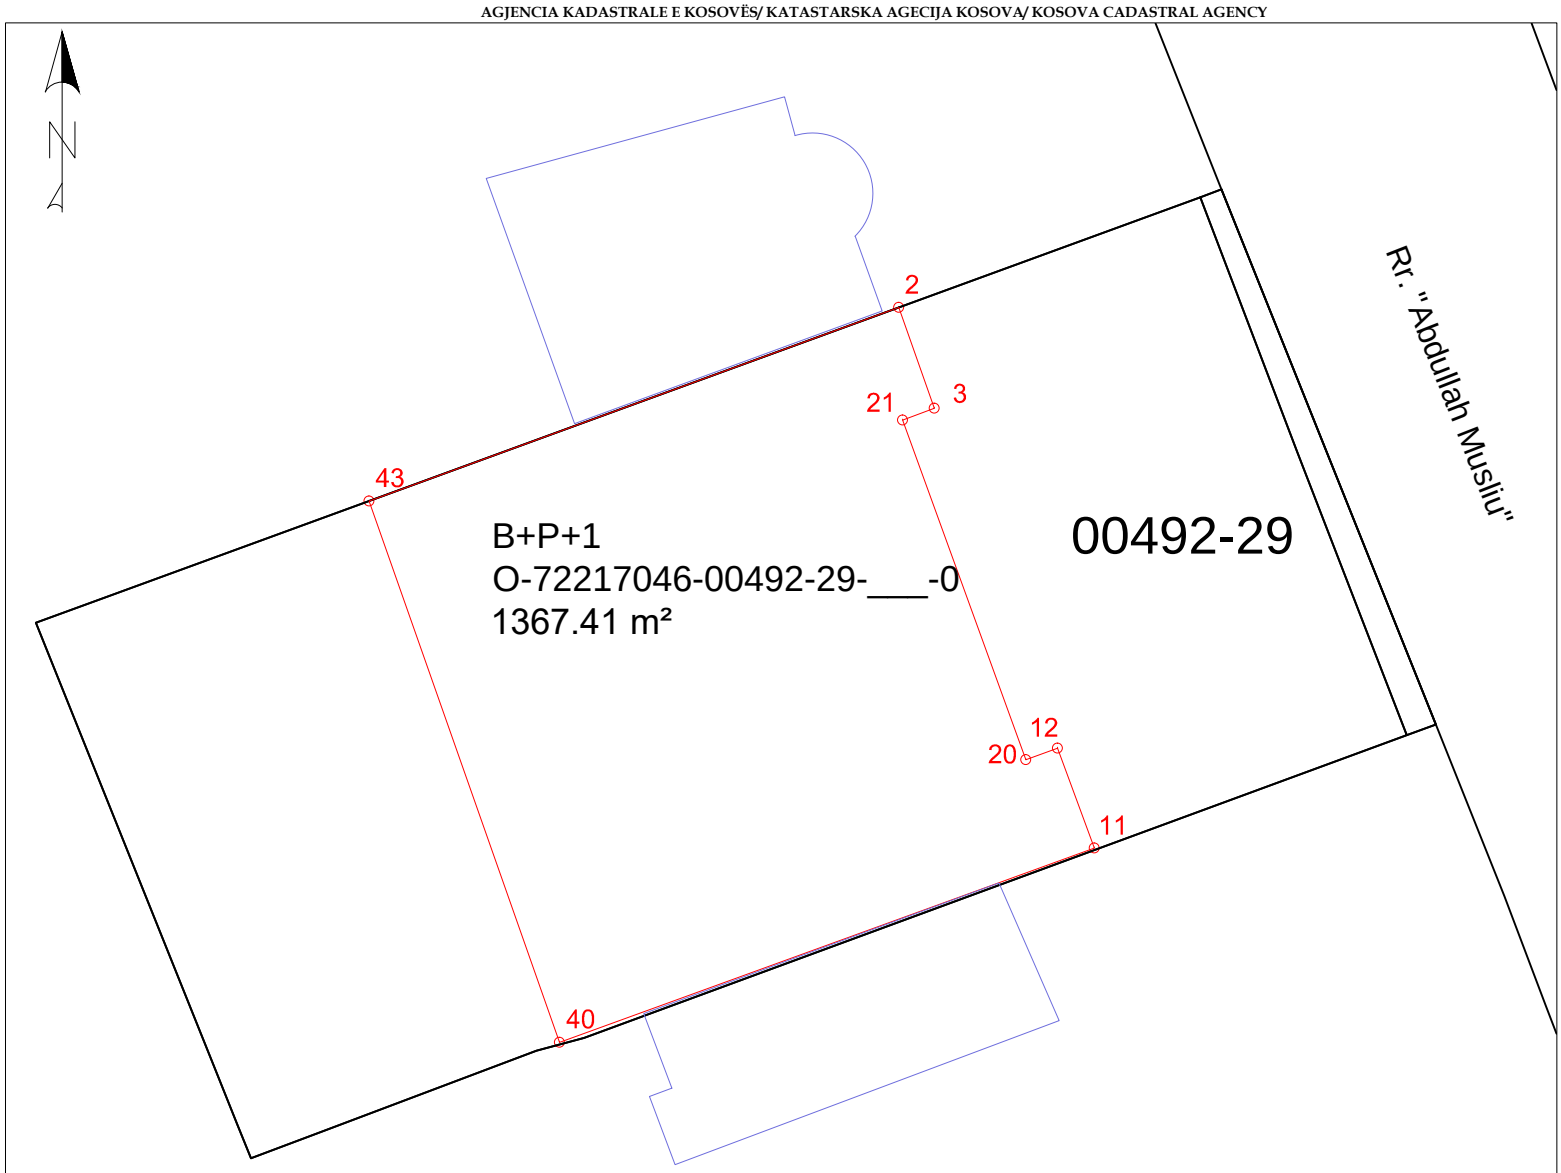

Nr	Y	X	H	Kodi	Përshkrimi	Burimi
2	7513447.573	4694382.782	620.200	40	Shtëpi-Ndërtesë	PM
3	7513449.933	4694376.116	620.200	40	Shtëpi-Ndërtesë	PM
11	7513460.511	4694347.031	620.200	40	Shtëpi-Ndërtesë	PM
12	7513458.081	4694353.646	620.200	40	Shtëpi-Ndërtesë	PM
20	7513455.970	4694352.871	620.200	40	Shtëpi-Ndërtesë	PM
21	7513447.831	4694375.329	620.200	40	Shtëpi-Ndërtesë	PM
40	7513425.152	4694334.202	620.200	40	Shtëpi-Ndërtesë	PM
43	7513412.544	4694369.979	620.200	40	Shtëpi-Ndërtesë	PM

Rilevoi / Snimio: LIRIDON SEJDIU

(emri dhe mbiemri i gjeodetit/kompanisë/ ime i prezime geodeta/ kompanije)

Nr. i licencës / Br. licence: 140

Nënshkrimi / Potpis: _____

Data e rilevimit / Datum snimanja: 13.08.2026

V.V.

Aprovoi / Usvojio: _____

(emri dhe mbiemri i përsonit zyrtar/ ime i prezime sluzbenog lica)

Nënshkrimi / Potpis: _____

Data e rilevimit / Datum snimanja: _____