
Nr	Y	X	H	Kodi	Përshkrimi	Burimi
2	7513447.573	4694382.782	620.200	40	Shtëpi-Ndërtesë	PM
3	7513449.933	4694376.116	620.200	40	Shtëpi-Ndërtesë	PM
11	7513460.511	4694347.031	620.200	40	Shtëpi-Ndërtesë	PM
12	7513458.081	4694353.646	620.200	40	Shtëpi-Ndërtesë	PM
20	7513455.970	4694352.871	620.200	40	Shtëpi-Ndërtesë	PM
21	7513447.831	4694375.329	620.200	40	Shtëpi-Ndërtesë	PM
40	7513425.152	4694334.202	620.200	40	Shtëpi-Ndërtesë	PM
43	7513412.544	4694369.979	620.200	40	Shtëpi-Ndërtesë	PM

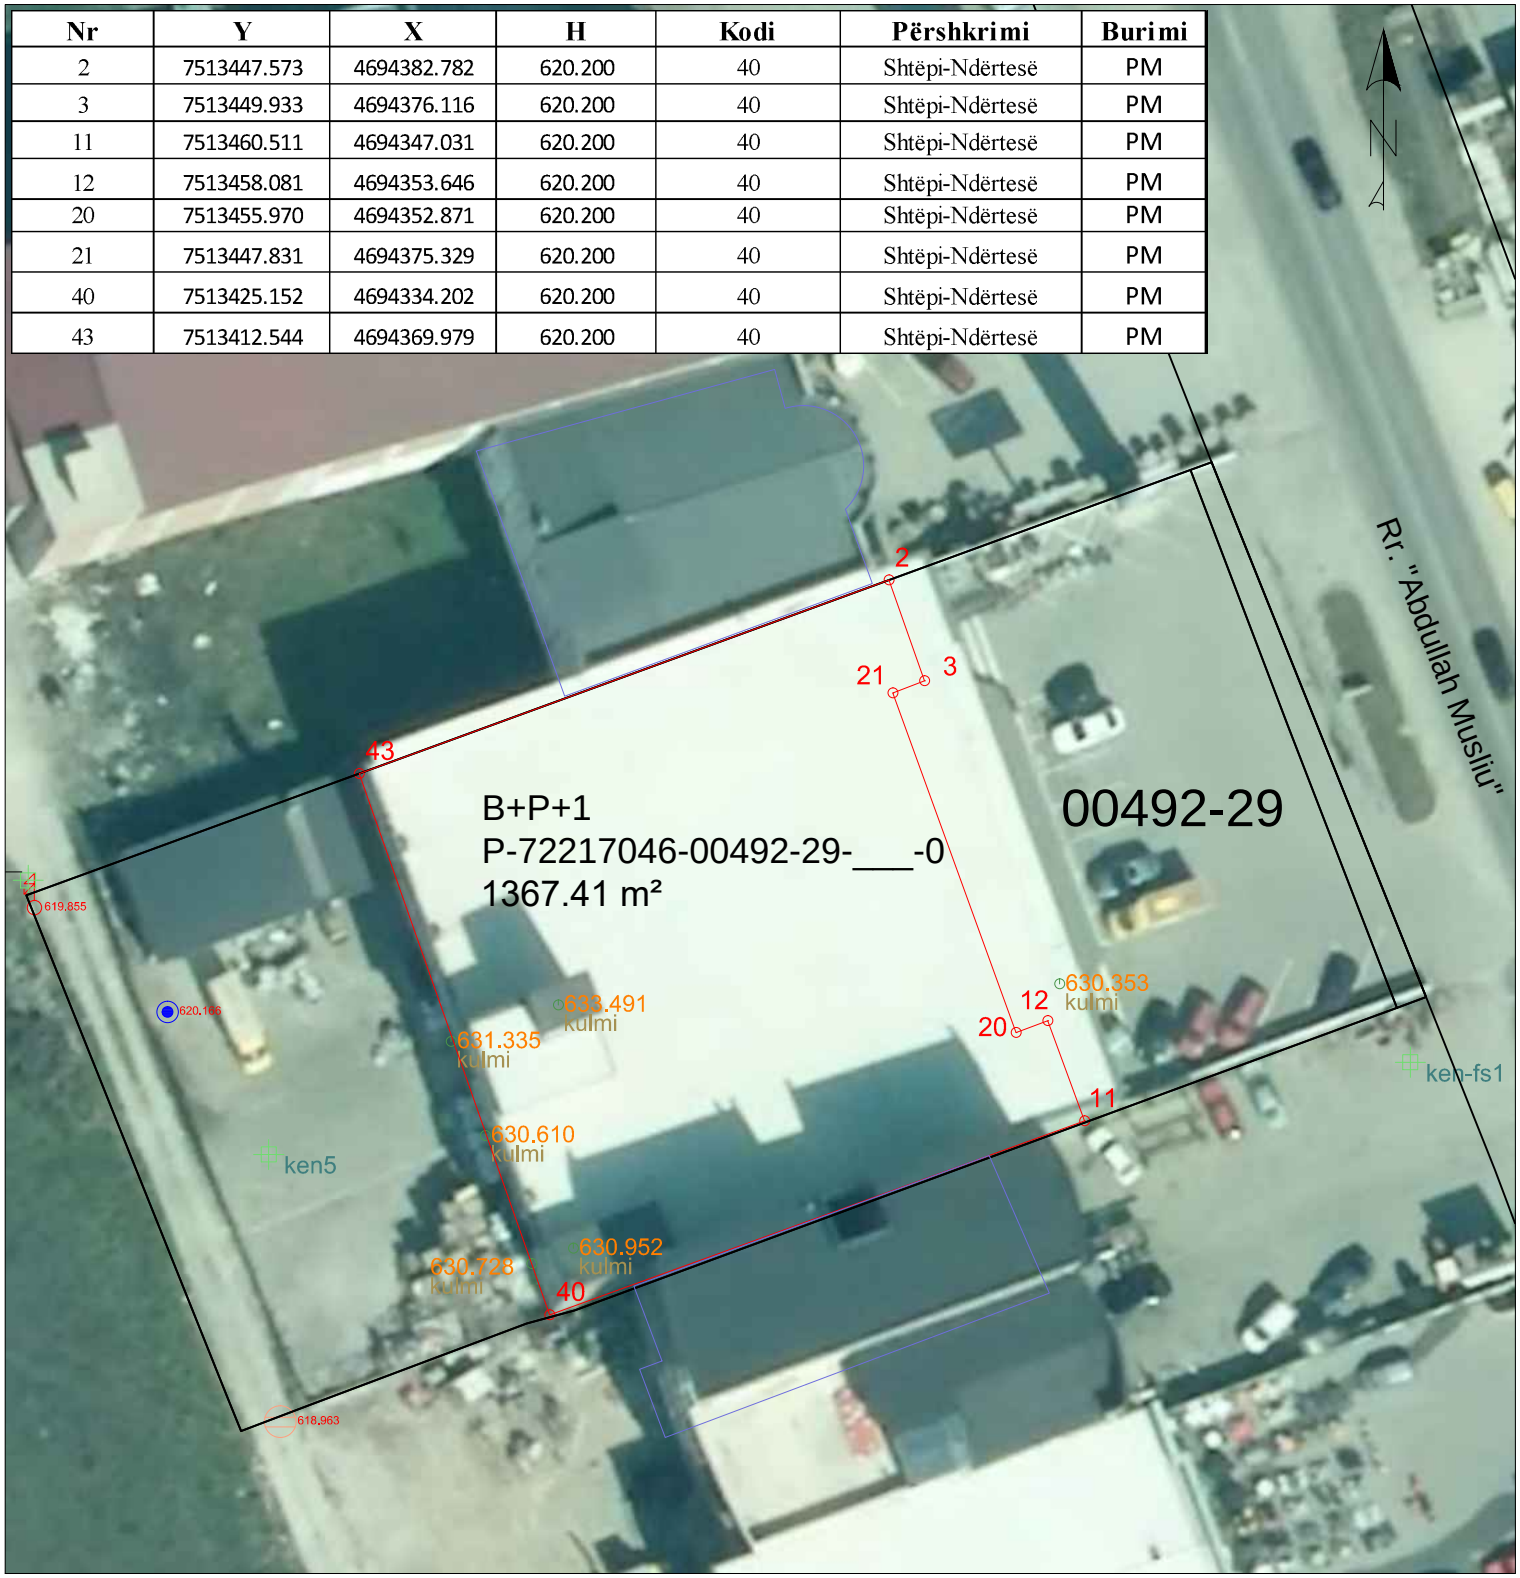

Republika e Kosovës

Qeveria -Vlada

Ministria e Mjedisit dhe Planifikimit Hapësinr /Ministarstv Sredine i Prstrng Planiranja

AGJENCIA KADASTRALE E KOSOVËS/ KATASTARSKA AGENCIJA KOSOVA

Situacioni i terrenit

Orto 2018

Zyra kadastrale kmunale / pštinska katastarska kancelarija: Ferizaj

Zona kadastrale / Katastarska zona: Talinoci i Jerlive

Nr. i njësisë kadastrale / Br. katastarske jedinice : 00492-29

Numri i lëndës / Broj predmeta: _____

Shkalla e zvoglimit / Razmera plana 1: 500

Lista e koordinatave të pikave të matura:

Nr	Y	X	H	DSC
56	7513390.661	4694362.930	620.655	ken_fs2
57	7513532.122	4694300.356	619.445	ken1
58	7513522.304	4694381.455	619.753	ken2
59	7513476.344	4694438.536	619.520	ken3
60	7513428.173	4694279.029	619.232	ken4
61	7513406.566	4694344.805	619.051	ken5
62	7513375.754	4694393.126	619.015	ken6
63	7513482.047	4694350.904	621.342	ken-fs1
31	7513458.846	4694356.071	630.353	kulmi
49	7513425.704	4694354.691	633.491	kulmi
50	7513418.633	4694352.277	631.335	kulmi
51	7513420.880	4694346.056	630.610	kulmi
52	7513423.952	4694337.586	630.728	kulmi
53	7513426.705	4694338.604	630.952	kulmi
39	7513391.067	4694361.118	619.855	kyqje_rryme
37	7513399.863	4694354.224	620.166	kyqje_uji
2	7513447.573	4694382.782	620.200	perdhese
3	7513449.933	4694376.116	620.200	perdhese
11	7513460.511	4694347.031	620.200	perdhese
12	7513458.081	4694353.646	620.200	perdhese
20	7513455.970	4694352.871	620.200	perdhese
21	7513447.831	4694375.329	620.200	perdhese
40	7513425.152	4694334.202	620.200	perdhese
43	7513412.544	4694369.979	620.200	perdhese
36	7513407.327	4694327.131	618.963	pusetFeekkal

Shpjegues:

- Kufiri kadastral (nga SIKTK-G)
- Ndërtesa në trajtim për legalizim
- Ndërtesa tjera
- Aneks Ndërtimi
- Shtyllë elektrike
- Pusetë e ujësjellësit
- Pusetë e ujërave të zeza
- Strehët
- Kyqje në rrymë
- Pikë e objekteve fqinje
- Rr. Emri i rrugës
- Pikë e rrjetës gjeodezike
- Pikë e strehëve
- 81 Pikë e terasës
- 10 Pikë e objektit
- Pikë e murit
- Pikë e kulmit

Rilevoi / Snimi: LIRIDON SEJDIU

(emri dhe mbiemri i gjedetit/kompanisë/ ime i prezime gedeta/ kompanije)

Nr. i licencës / Br. licence: 140

Data e rilevimit / Datum snimanja: 13.08.2026

Nënshkrimi / Potpis: _____

V.V.