Zyra kadastrale komunale / Opštinska katastarska kancelarija: Ferizaj

Zona kadastrale / Katastarska zona: Talinoci i Jerlive

Lloji i njësisë kadastrale / Vrsta katastarske jedinice : Ndërtesë

Nr. i njësisë kadastrale / Br. katastarske jedinice : 00492-29

Numri i lëndës / Broj predmeta: _____

Shkalla e zvoglimit / Razmera plana 1: 500


Republika e Kosovës

Republika Kosova-Republic of Kosova

Qeveria -Vlada-Government

Ministria e Mjedisit dhe Planifikimit Hapësinor /Ministarstvo Sredine i Prostornog Planiranja/Ministry of Environment and Spatial Planning

AGJENCIA KADASTRALE E KOSOVËS/ KATASTARSKA AGECIJA KOSOVA/ KOSOVA CADASTRAL AGENCY

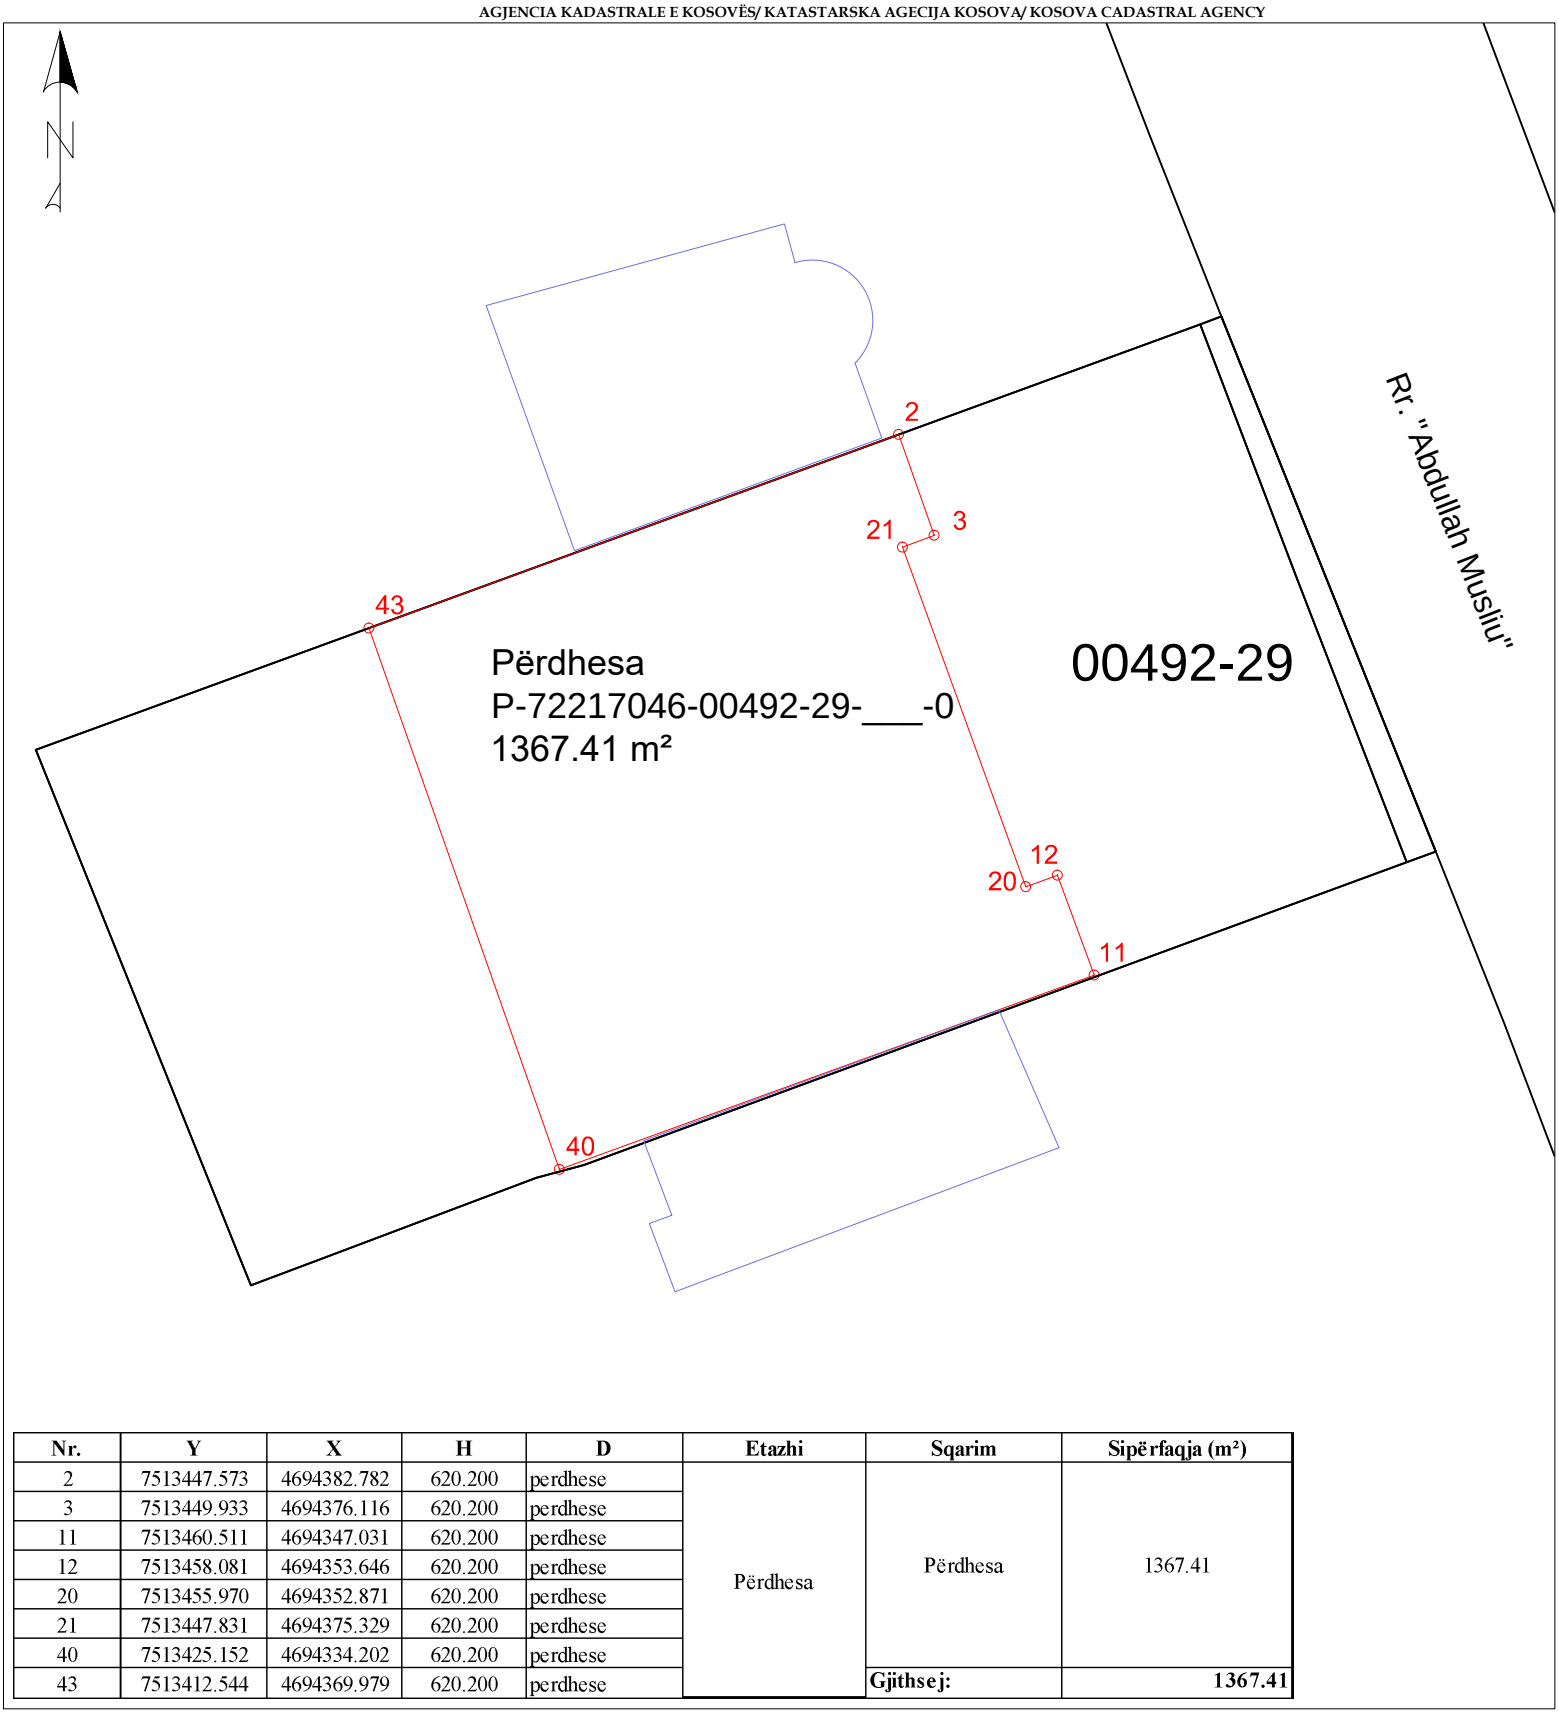

Nr.	Y	X	H	D	Etazhi	Sqarim	Sipërfaqja (m²)
2	7513447.573	4694382.782	620.200	perdhese	Përdhesa	Përdhesa	1367.41
3	7513449.933	4694376.116	620.200	perdhese			
11	7513460.511	4694347.031	620.200	perdhese			
12	7513458.081	4694353.646	620.200	perdhese			
20	7513455.970	4694352.871	620.200	perdhese			
21	7513447.831	4694375.329	620.200	perdhese			
40	7513425.152	4694334.202	620.200	perdhese			
43	7513412.544	4694369.979	620.200	perdhese		**Gjithsej:**	**1367.41**

Rilevoi / Snimio: LIRIDON SEJDIU

(emri dhe mbiemri i gjeodetit/kompanisë/ ime i prezime geodeta/ kompanije)

Nr. i licencës / Br. licence: 140

Nënshkrimi / Potpis: _____

Data e rilevimit / Datum snimanja: 13.08.2026

V.V.

Aprovoi / Usvojio: _____

(emri dhe mbiemri i përsonit zyrtar/ ime i prezime sluzbenog lica)

Nënshkrimi / Potpis: _____

Data e rilevimit / Datum snimanja: _____