Zyra kadastrale komunale / Opštinska katastarska kancelarija: Ferizaj

Nr. i njësisë kadastrale / Br. katastarske jedinice : 00492-29

Zona kadastrale / Katastarska zona: Talinoci i Jerlive

Numri i lëndës / Broj predmeta:

Lloji i njësisë kadastrale / Vrsta katastarske jedinice : Ndërtesë

Shkalla e zvoglimit / Razmera plana 1: 500


Republika e Kosovës

Republika Kosova-Republic of Kosova

Qeveria -Vlada-Government

Ministria e Mjedisit dhe Planifikimit Hapësinor /Ministarstvo Sredine i Prostornog Planiranja/Ministry of Environment and Spatial Planning

AGJENCIA KADASTRALE E KOSOVËS/ KATASTARSKA AGECIJA KOSOVA/ KOSOVA CADASTRAL AGENCY

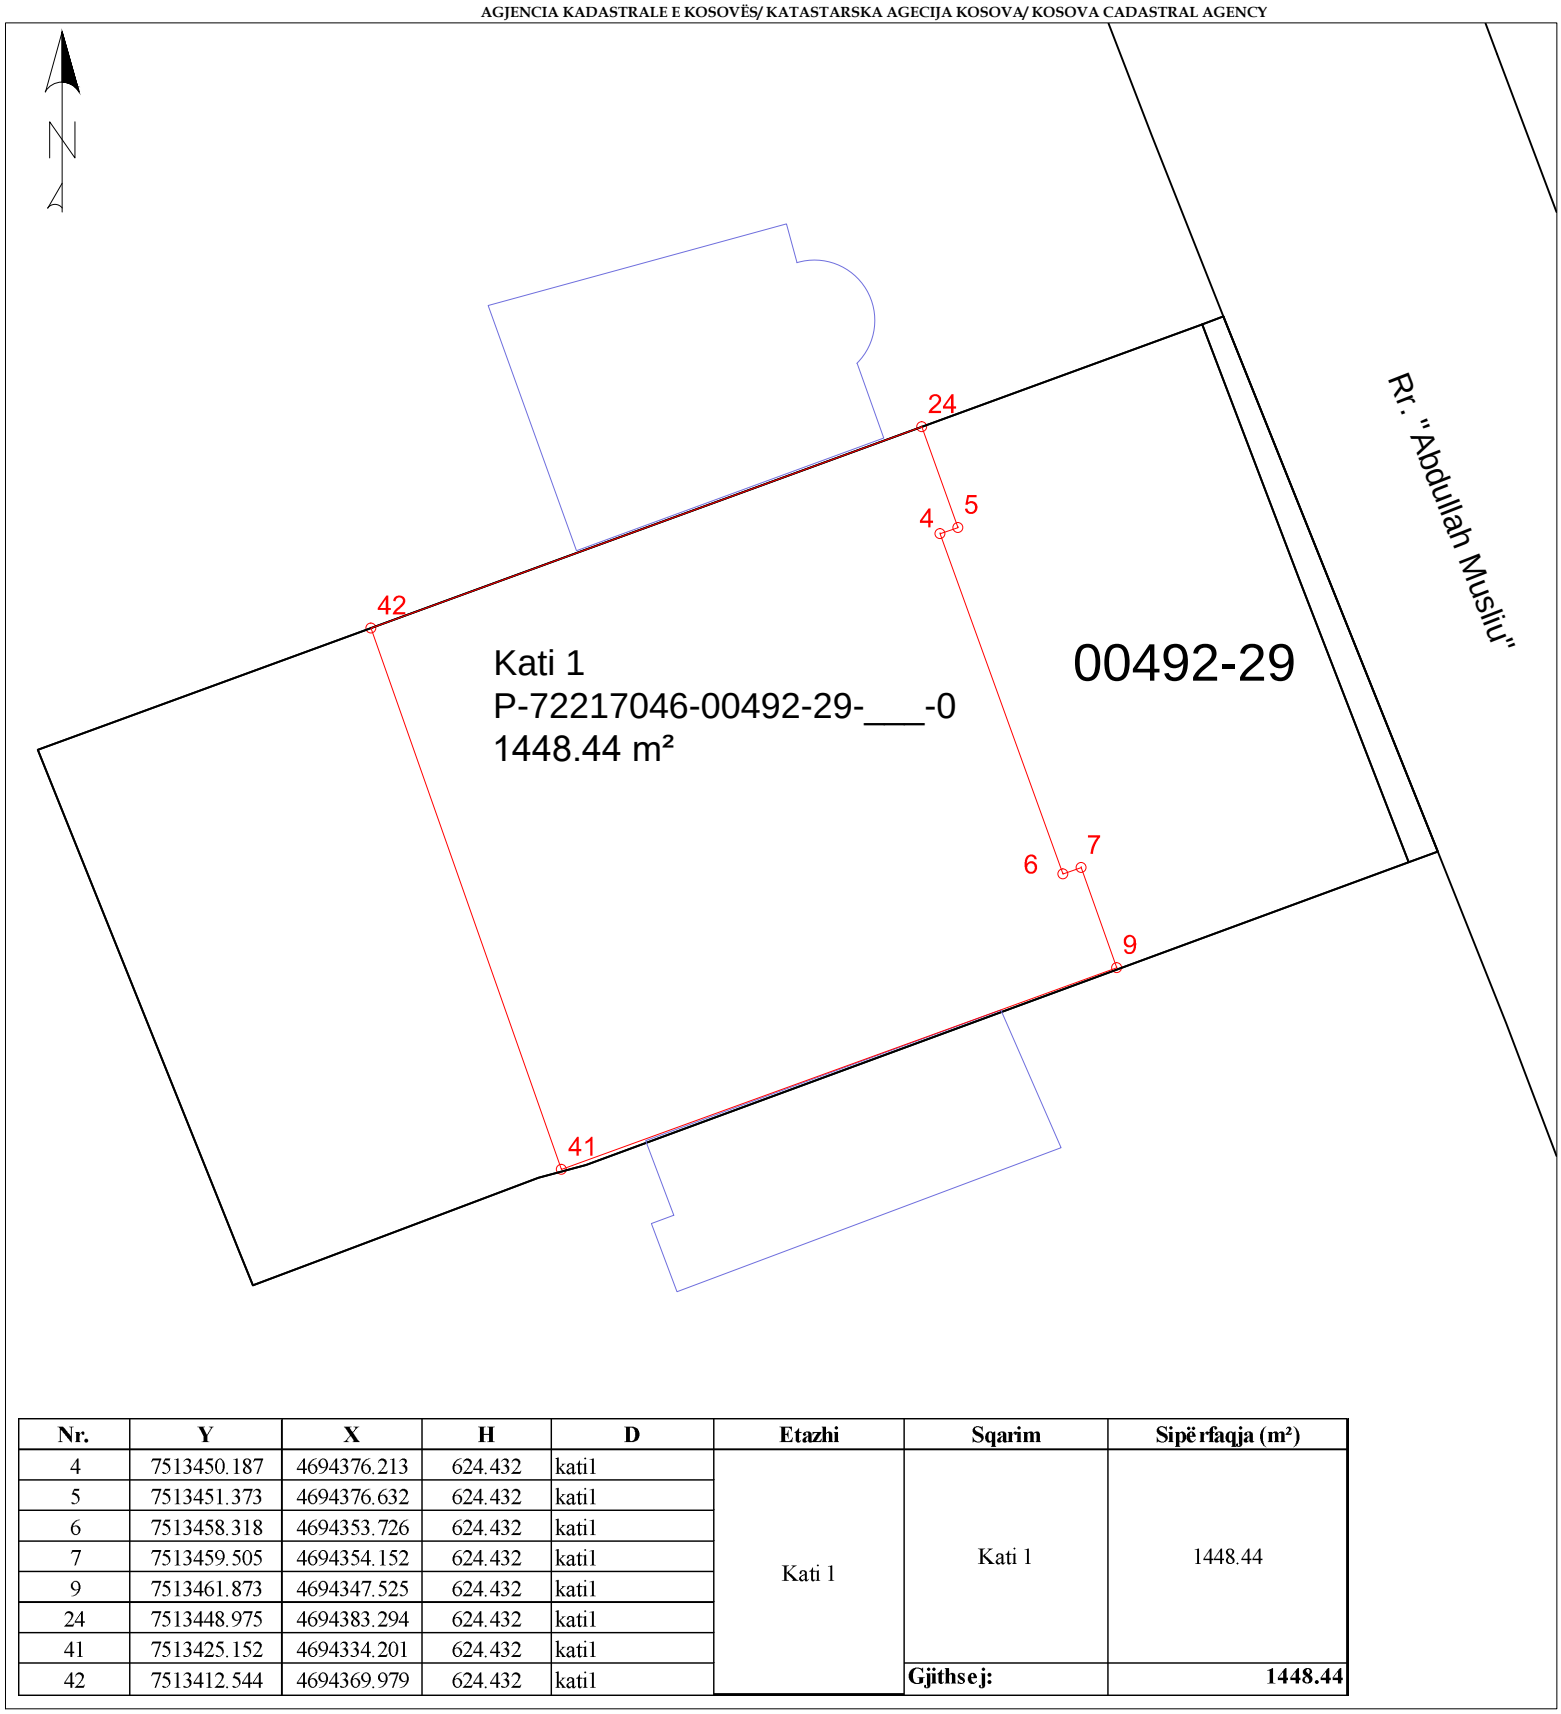

Nr.	Y	X	H	D	Etazhi	Sqarim	Sipërfaqja (m²)
4	7513450.187	4694376.213	624.432	kati1	Kati 1	Kati 1	1448.44
5	7513451.373	4694376.632	624.432	kati1			
6	7513458.318	4694353.726	624.432	kati1			
7	7513459.505	4694354.152	624.432	kati1			
9	7513461.873	4694347.525	624.432	kati1			
24	7513448.975	4694383.294	624.432	kati1			
41	7513425.152	4694334.201	624.432	kati1			
42	7513412.544	4694369.979	624.432	kati1		**Gjithsej:**	**1448.44**

Rilevoi / Snimio: LIRIDON SEJDIU

(emri dhe mbiemri i gjeodetit/kompanisë/ ime i prezime geodeta/ kompanije)

Nr. i licencës / Br. licence: 140

Nënshkrimi / Potpis:

Data e rilevimit / Datum snimanja: 13.08.2026

V.V.

Aprovoi / Usvojio:

(emri dhe mbiemri i përsonit zyrtar/ ime i prezime sluzbenog lica)

Nënshkrimi / Potpis:

Data e rilevimit / Datum snimanja: