
Nr	Y	X	H	Kodi	Përshkrimi	Burimi
2	7513447.573	4694382.782	620.200	40	Shtëpi-Ndërtesë	PM
3	7513449.933	4694376.116	620.200	40	Shtëpi-Ndërtesë	PM
11	7513460.511	4694347.031	620.200	40	Shtëpi-Ndërtesë	PM
12	7513458.081	4694353.646	620.200	40	Shtëpi-Ndërtesë	PM
20	7513455.970	4694352.871	620.200	40	Shtëpi-Ndërtesë	PM
21	7513447.831	4694375.329	620.200	40	Shtëpi-Ndërtesë	PM
40	7513425.152	4694334.202	620.200	40	Shtëpi-Ndërtesë	PM
43	7513412.544	4694369.979	620.200	40	Shtëpi-Ndërtesë	PM

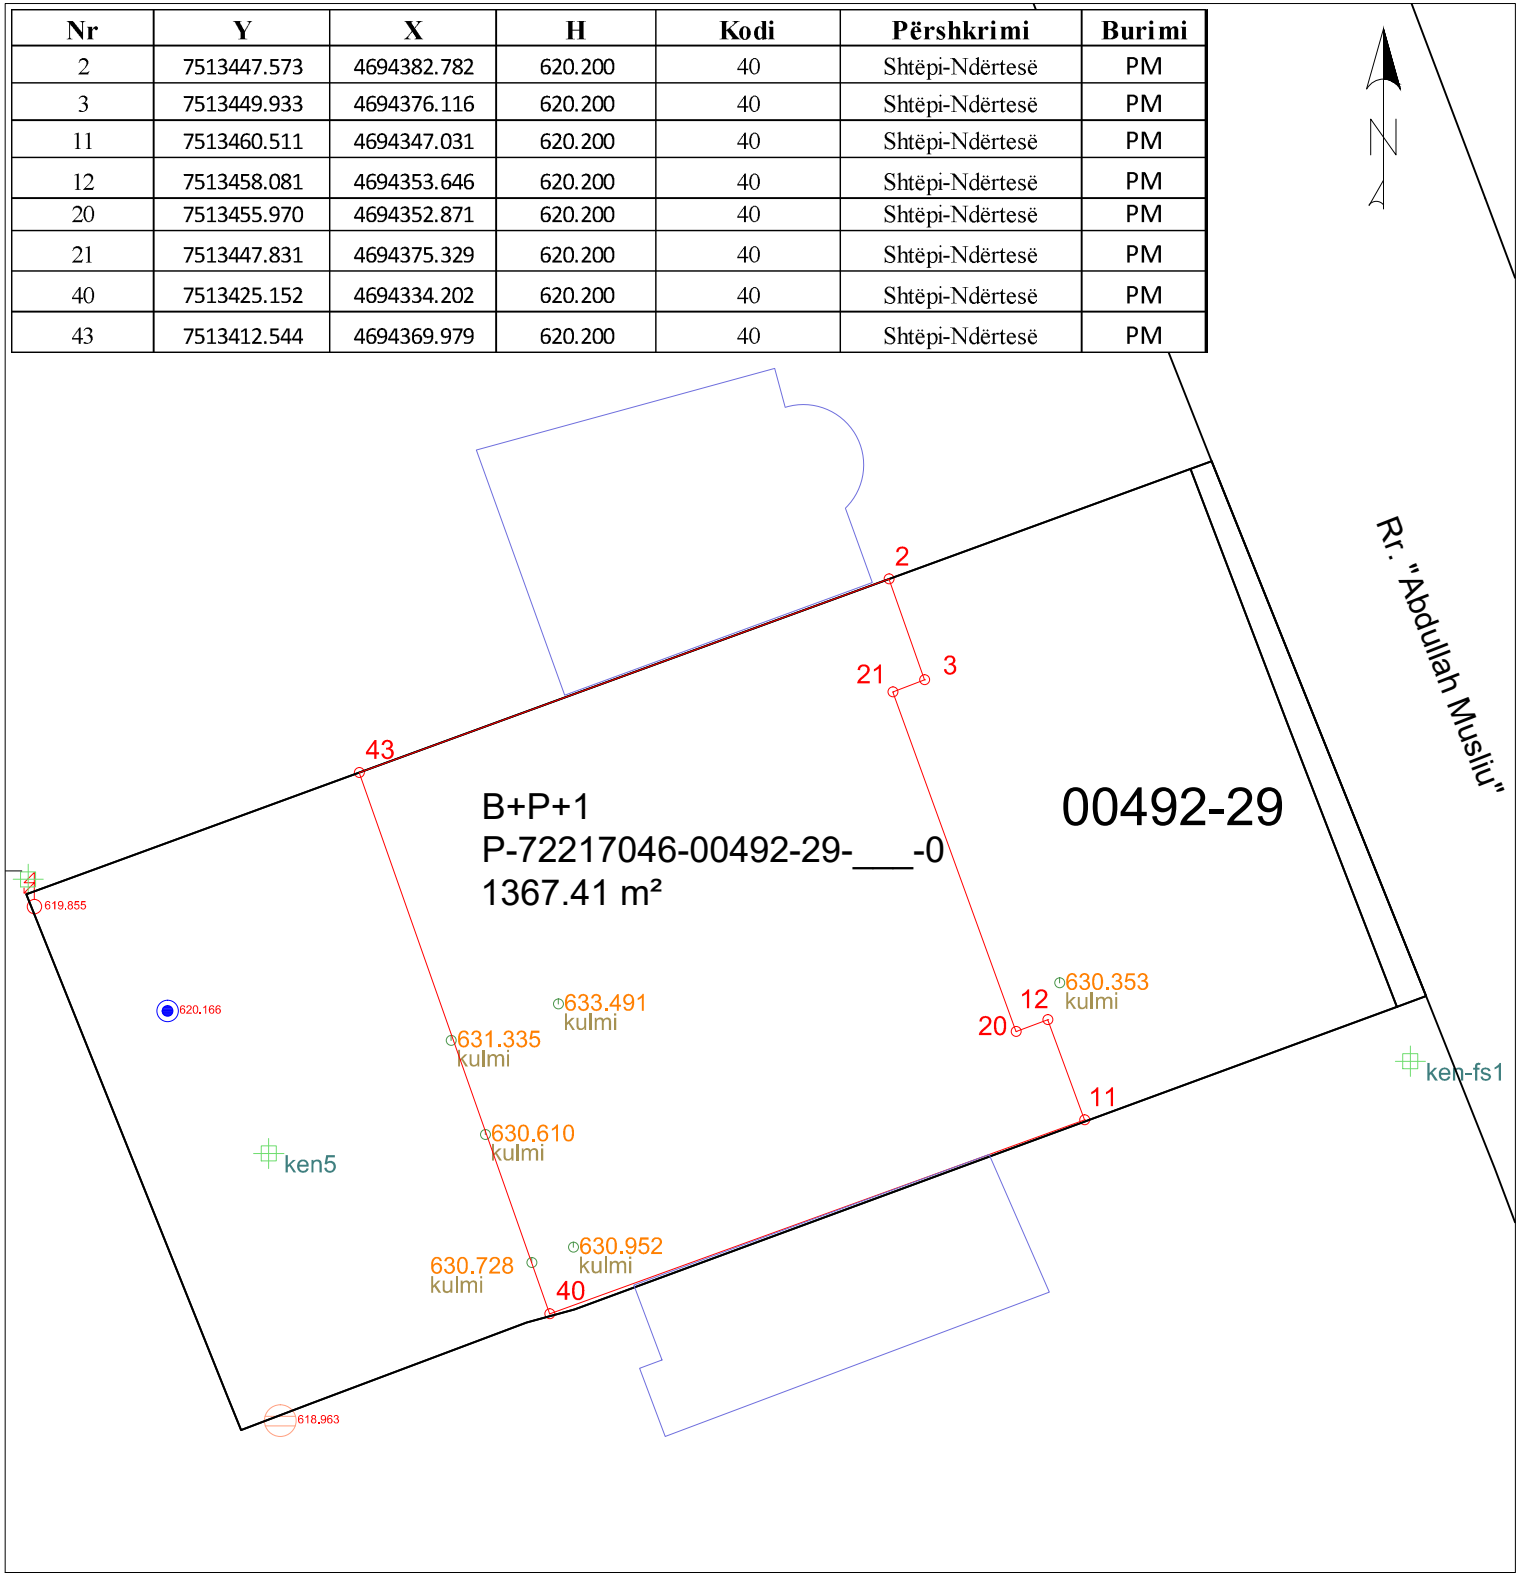

Republika e Kosovës

Qeveria -Vlada

Ministria e Mjedisit dhe Planifikimit Hapësinr /Ministarstv Sredine i Prstrng Planiranja

AGJENCIA KADASTRALE E KOSOVËS/ KATASTARSKA AGENCIJA KOSOVA

Situacioni i terrenit

Orto 2018

Zyra kadastrale kmunale / pštinska katastarska kancelarija: Ferizaj

Zona kadastrale / Katastarska zona: Talinoci i Jerlive

Nr. i njësisë kadastrale / Br. katastarske jedinice : 00492-29

Numri i lëndës / Broj predmeta: _____

Shkalla e zvoglimit / Razmera plana 1: 500

Lista e koordinatave të pikave të matura:

Nr	Y	X	H	DSC
56	7513390.661	4694362.930	620.655	ken_fs2
57	7513532.122	4694300.356	619.445	ken1
58	7513522.304	4694381.455	619.753	ken2
59	7513476.344	4694438.536	619.520	ken3
60	7513428.173	4694279.029	619.232	ken4
61	7513406.566	4694344.805	619.051	ken5
62	7513375.754	4694393.126	619.015	ken6
63	7513482.047	4694350.904	621.342	ken-fs1
31	7513458.846	4694356.071	630.353	kulmi
49	7513425.704	4694354.691	633.491	kulmi
50	7513418.633	4694352.277	631.335	kulmi
51	7513420.880	4694346.056	630.610	kulmi
52	7513423.952	4694337.586	630.728	kulmi
53	7513426.705	4694338.604	630.952	kulmi
39	7513391.067	4694361.118	619.855	kyqje_rryme
37	7513399.863	4694354.224	620.166	kyqje_uji
2	7513447.573	4694382.782	620.200	perdhese
3	7513449.933	4694376.116	620.200	perdhese
11	7513460.511	4694347.031	620.200	perdhese
12	7513458.081	4694353.646	620.200	perdhese
20	7513455.970	4694352.871	620.200	perdhese
21	7513447.831	4694375.329	620.200	perdhese
40	7513425.152	4694334.202	620.200	perdhese
43	7513412.544	4694369.979	620.200	perdhese
36	7513407.327	4694327.131	618.963	pusetFeekkal

Shpjegues:

- Kufiri kadastral (nga SIKTK-G)
- Ndërtesa në trajtim për legalizim
- Ndërtesa tjera
- Aneks Ndërtimi
- Shtyllë elektrike
- Pusetë e ujësjellësit
- Pusetë e ujërave të zeza
- Strehët
- Kyqje në rrymë
- Pikë e objekteve fqinje
- Rr. Emri i rrugës
- Pikë e rrjetës gjeodezike
- Pikë e strehëve
- 81 Pikë e terasës
- 10 Pikë e objektit
- Pikë e murit
- Pikë e kulmit

Rilevoi / Snimi: LIRIDON SEJDIU

(emri dhe mbiemri i gjedetit/kompanisë/ ime i prezime gedeta/ kompanije)


Nr. i licencës / Br. licence: 140

Data e rilevimit / Datum snimanja: 13.08.2026

Nënshkrimi / Potpis: _____

V.V.

Nr	Y	X	H	Kodi	Përshkrimi	Burimi
2	7513447.573	4694382.782	620.200	40	Shtëpi-Ndërtesë	PM
3	7513449.933	4694376.116	620.200	40	Shtëpi-Ndërtesë	PM
11	7513460.511	4694347.031	620.200	40	Shtëpi-Ndërtesë	PM
12	7513458.081	4694353.646	620.200	40	Shtëpi-Ndërtesë	PM
20	7513455.970	4694352.871	620.200	40	Shtëpi-Ndërtesë	PM
21	7513447.831	4694375.329	620.200	40	Shtëpi-Ndërtesë	PM
40	7513425.152	4694334.202	620.200	40	Shtëpi-Ndërtesë	PM
43	7513412.544	4694369.979	620.200	40	Shtëpi-Ndërtesë	PM

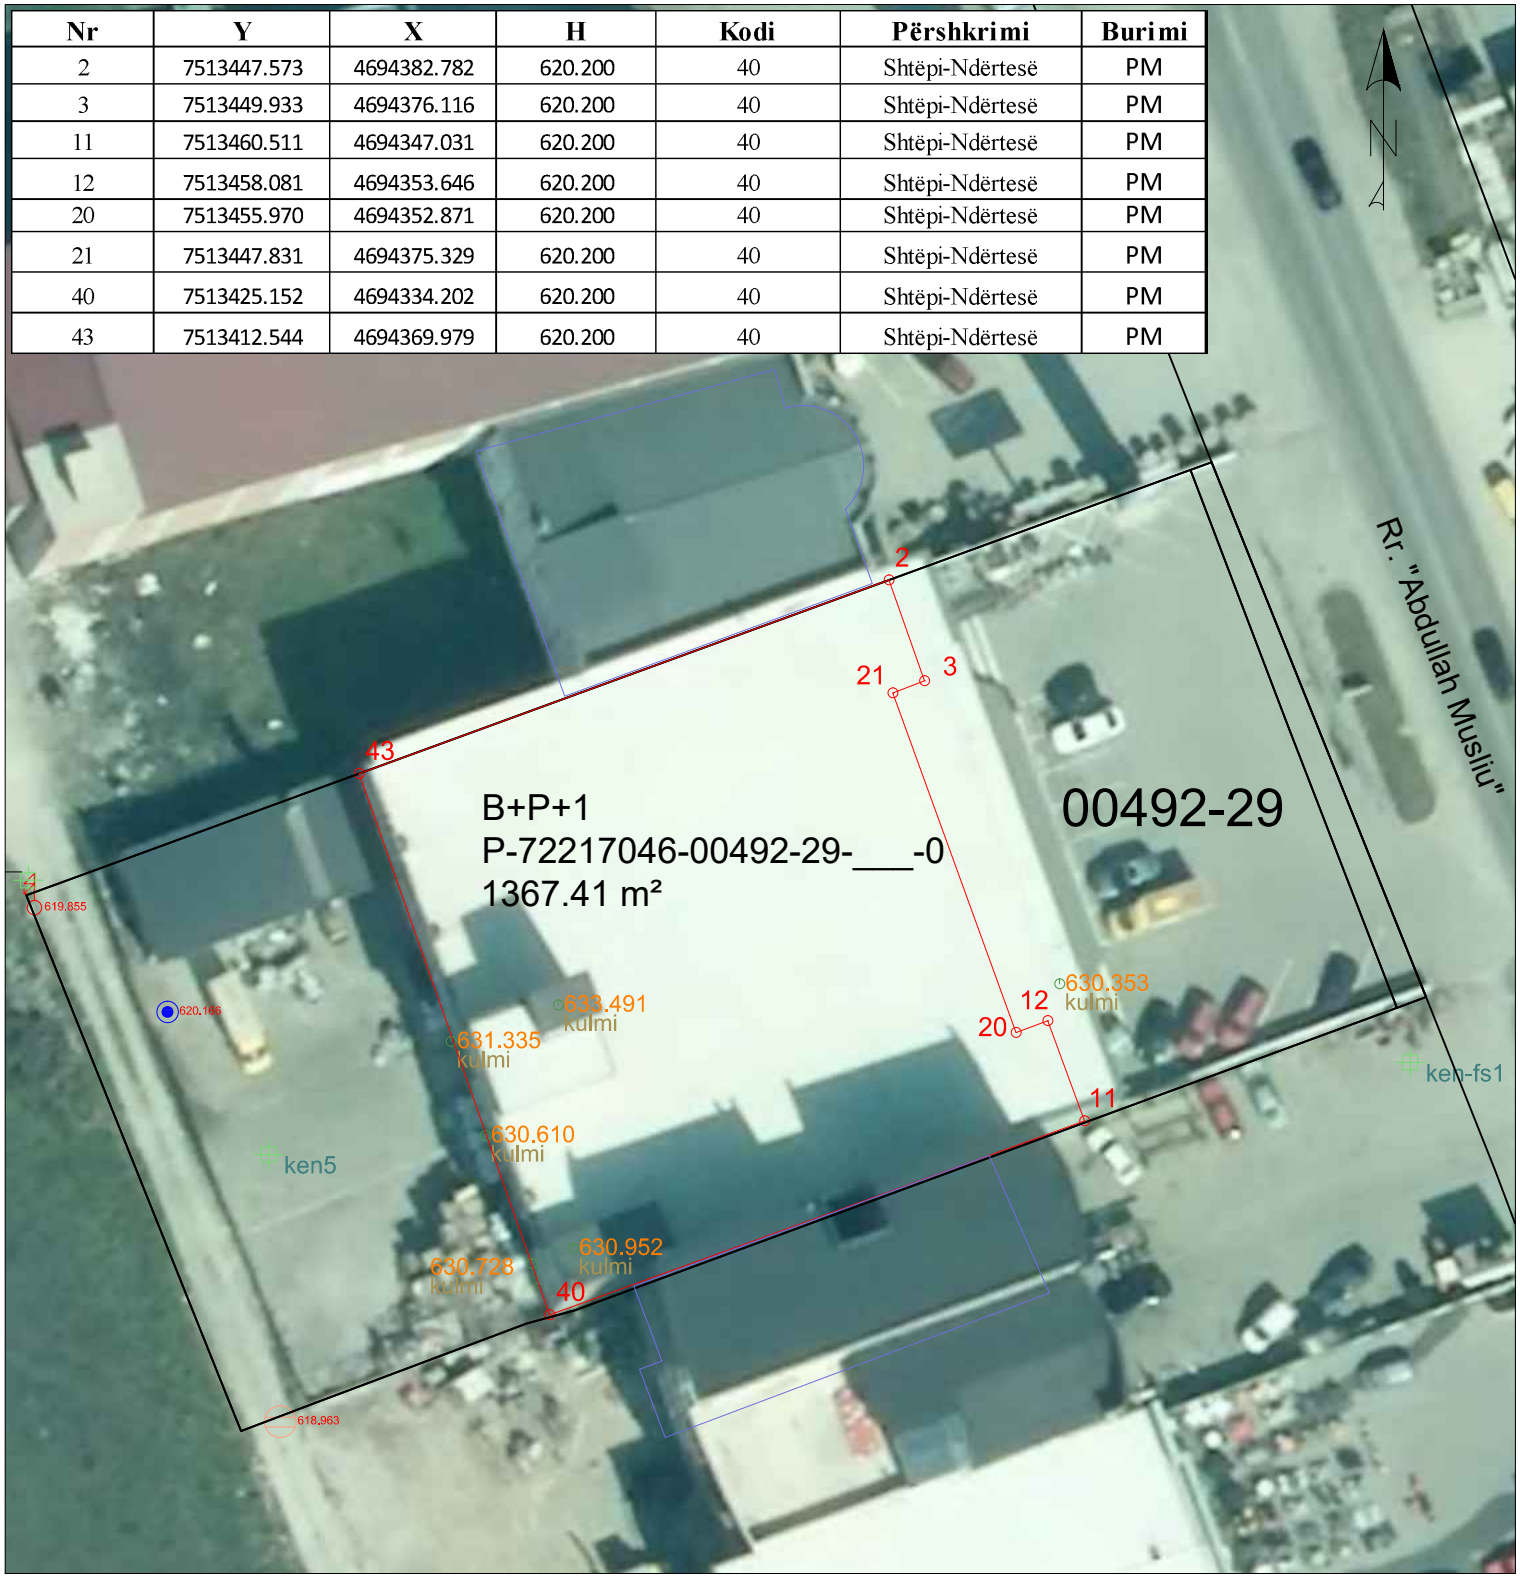

Republika e Kosovës

Qeveria -Vlada

Ministria e Mjedisit dhe Planifikimit Hapësinr /Ministarstv Sredine i Prstrng Planiranja

AGJENCIA KADASTRALE E KOSOVËS/ KATASTARSKA AGENCIJA KOSOVA

Situacioni i terrenit

Orto 2018

Zyra kadastrale kmunale / pštinska katastarska kancelarija: Ferizaj

Zona kadastrale / Katastarska zona: Talinoci i Jerlive

Nr. i njësisë kadastrale / Br. katastarske jedinice : 00492-29

Numri i lëndës / Broj predmeta: _____

Shkalla e zvoglimit / Razmera plana 1: 500

Lista e koordinatave të pikave të matura:

Nr	Y	X	H	DSC
56	7513390.661	4694362.930	620.655	ken_fs2
57	7513532.122	4694300.356	619.445	ken1
58	7513522.304	4694381.455	619.753	ken2
59	7513476.344	4694438.536	619.520	ken3
60	7513428.173	4694279.029	619.232	ken4
61	7513406.566	4694344.805	619.051	ken5
62	7513375.754	4694393.126	619.015	ken6
63	7513482.047	4694350.904	621.342	ken-fs1
31	7513458.846	4694356.071	630.353	kulmi
49	7513425.704	4694354.691	633.491	kulmi
50	7513418.633	4694352.277	631.335	kulmi
51	7513420.880	4694346.056	630.610	kulmi
52	7513423.952	4694337.586	630.728	kulmi
53	7513426.705	4694338.604	630.952	kulmi
39	7513391.067	4694361.118	619.855	kyqje_rryme
37	7513399.863	4694354.224	620.166	kyqje_uji
2	7513447.573	4694382.782	620.200	perdhese
3	7513449.933	4694376.116	620.200	perdhese
11	7513460.511	4694347.031	620.200	perdhese
12	7513458.081	4694353.646	620.200	perdhese
20	7513455.970	4694352.871	620.200	perdhese
21	7513447.831	4694375.329	620.200	perdhese
40	7513425.152	4694334.202	620.200	perdhese
43	7513412.544	4694369.979	620.200	perdhese
36	7513407.327	4694327.131	618.963	pusetFeekkal

Shpjegues:

- Kufiri kadastral (nga SIKTK-G)
- Ndërtesa në trajtim për legalizim
- Ndërtesa tjera
- Aneks Ndërtimi
- Shtyllë elektrike
- Pusetë e ujësjellësit
- Pusetë e ujërave të zeza
- Strehët
- Kyqje në rrymë
- Pikë e objekteve fqinje
- Rr. Emri i rrugës
- Pikë e rrjetës gjeodezike
- Pikë e strehëve
- 81 Pikë e terasës
- 10 Pikë e objektit
- Pikë e murit
- Pikë e kulmit

Rilevoi / Snimi: LIRIDON SEJDIU

(emri dhe mbiemri i gjedetit/kompanisë/ ime i prezime gedeta/ kompanije)

Nr. i licencës / Br. licence: 140

Data e rilevimit / Datum snimanja: 13.08.2026

Nënshkrimi / Potpis: _____

V.V.

Republika e Kosovës
Republika Kosova-Republic of Kosovo
Qeveria e Kosovës- Vlada Kosova- Government of Kosovo
Ministria e Infrastrukturës dhe Ambientit/ Ministrastvo Infrastrukture i Sredine/ Ministry of Infrastructure and Environment
AGJENCIA KADASTRALE E KOSOVËS/KOSOVSKA KATASTARSKA AGENCIJA/ KOSOVO CADASTRAL AGENCY

Komuna: Ferizaj	**Zona Kadastrale: Talinoc i Jerlive**
Numri i njësis kadastrale: 00492-29	**Sistemi koordinat: KosovaRef01**

Nr	Y	X	H	Kodi	Përshkrimi	Burimi
2	7513447.573	4694382.782	620.200	40	Shtëpi-Ndërtesë	PM
3	7513449.933	4694376.116	620.200	40	Shtëpi-Ndërtesë	PM
11	7513460.511	4694347.031	620.200	40	Shtëpi-Ndërtesë	PM
12	7513458.081	4694353.646	620.200	40	Shtëpi-Ndërtesë	PM
20	7513455.970	4694352.871	620.200	40	Shtëpi-Ndërtesë	PM
21	7513447.831	4694375.329	620.200	40	Shtëpi-Ndërtesë	PM
40	7513425.152	4694334.202	620.200	40	Shtëpi-Ndërtesë	PM
43	7513412.544	4694369.979	620.200	40	Shtëpi-Ndërtesë	PM

Gjeodeti / Kompania gjeodete e licencuar:	Liridon Sejdiu	Nënshkrimi dhe vula:	
Numri i licencës	140		

Republika e Kosovës
Republika Kosova - Republic of Kosovo
Qeveria - Vlada - Government
Ministria e Mjedisit dhe Planifikimit Hapësinor / Ministarstvo Životne Sredine i Prostornog Planiranja / Ministry of Environment and Spatial Planning
AGJENCIA KADASTRALE E KOSOVËS / KATASTARSKA AGENCIJA KOSOVA / KOSOVO CADASTRAL AGENCY

492-29-TalinocJerlive

Y: 7513333.236
X: 4694424.874

Y: 7513554.451
X: 4694424.874



Y: 7513333.236
X: 4694268.459

Y: 7513554.451
X: 4694268.459

1 : 1,082
0 46 8 m

Printuar më: 13.11.2026 09:02

Zyra kadastrale komunale / Opštinska katastarska kancelarija: Ferizaj

Nr. i njësisë kadastrale / Br. katastarske jedinice : 00492-29

Zona kadastrale / Katastarska zona: Talinoci i Jerlive

Numri i lëndës / Broj predmeta:

Lloji i njësisë kadastrale / Vrsta katastarske jedinice : Ndërtesë

Shkalla e zvoglimit / Razmera plana 1: 500


Republika e Kosovës

Republika Kosova-Republic of Kosova

Qeveria -Vlada-Government

Ministria e Mjedisit dhe Planifikimit Hapësinor /Ministarstvo Sredine i Prostornog Planiranja/Ministry of Environment and Spatial Planning

AGJENCIA KADASTRALE E KOSOVËS/ KATASTARSKA AGECIJA KOSOVA/ KOSOVA CADASTRAL AGENCY

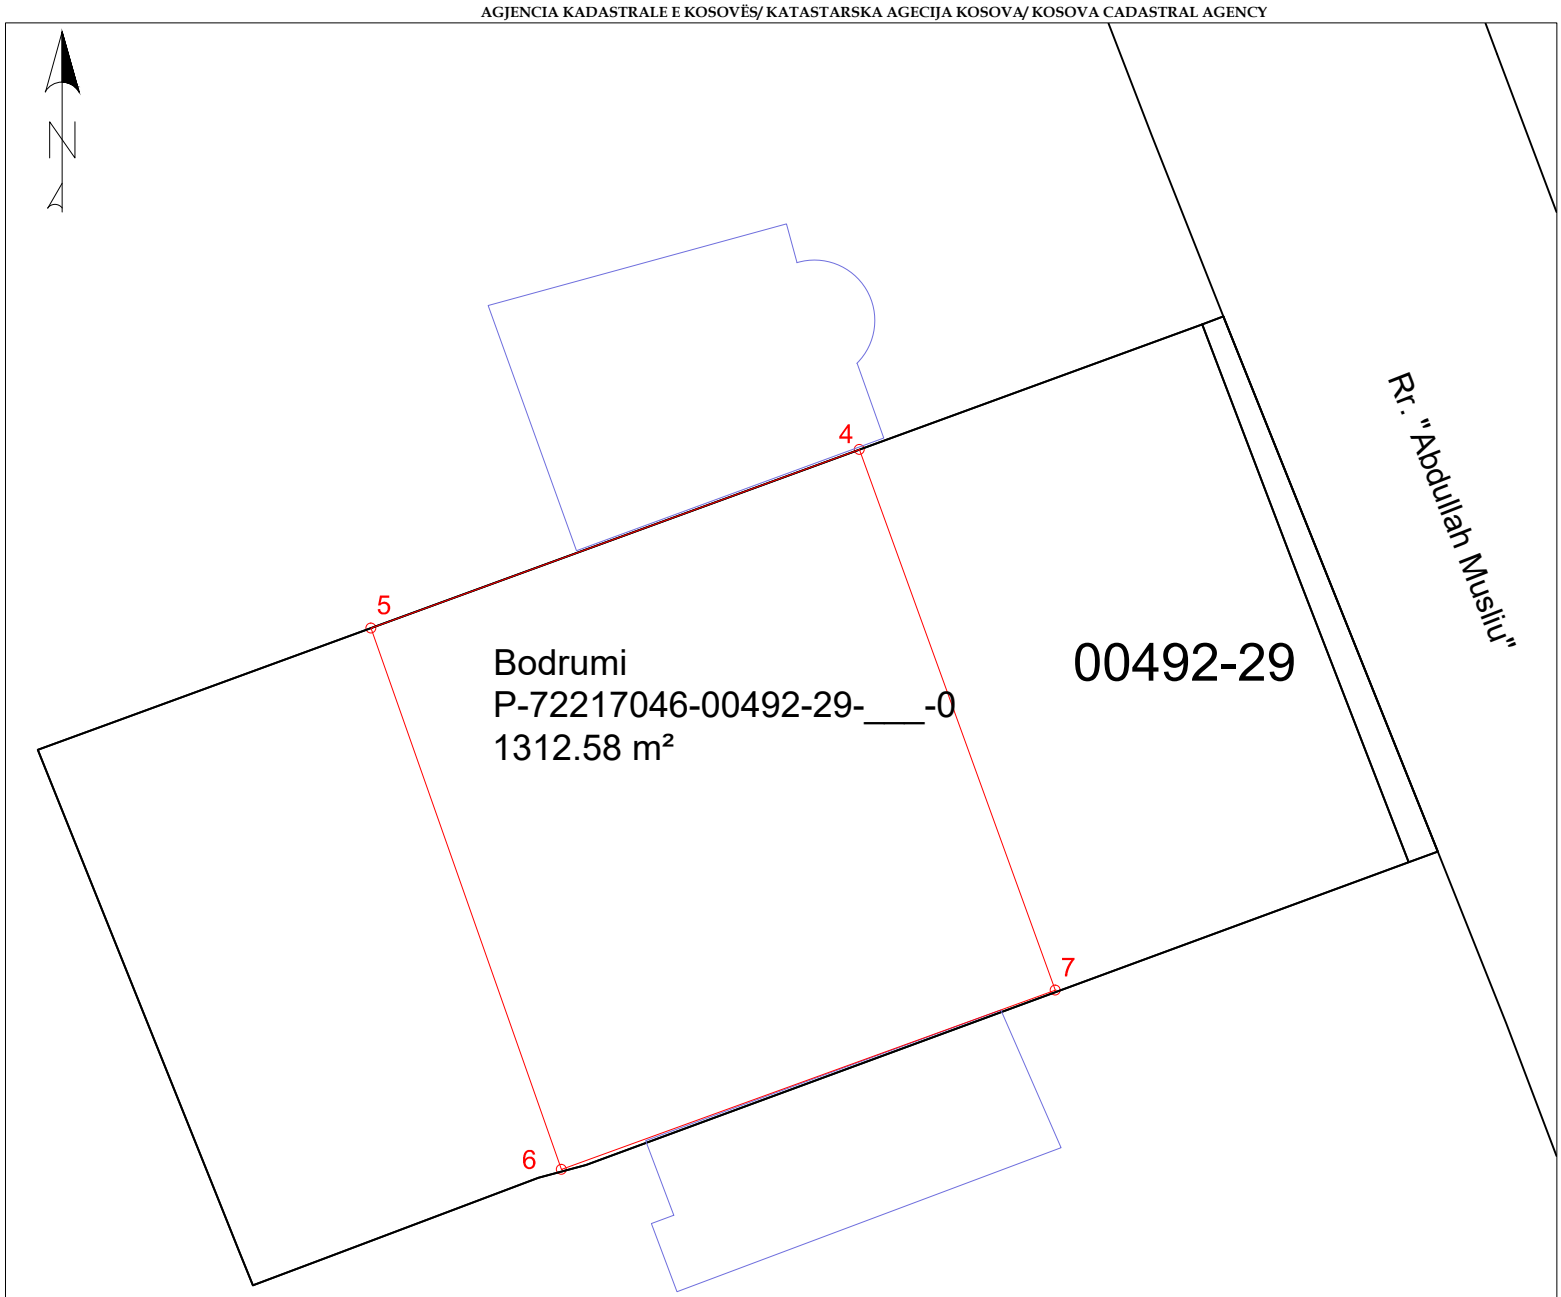

Nr.	Y	X	H	D	Etazhi	Sqarim	Sipërfaqja (m²)
4	7513444.852	4694381.788	617.000	Bodrumi	Bodrumi	Bodrumi	1312.58
5	7513412.544	4694369.979	617.000	Bodrumi			
6	7513425.152	4694334.202	617.000	Bodrumi			
7	7513457.804	4694346.049	617.000	Bodrumi		**Gjithsej:**	**1312.58**

Rilevoi / Snimio: LIRIDON SEJDIU

(emri dhe mbiemri i gjeodetit/kompanisë/ ime i prezime geodeta/ kompanije)

Nr. i licencës / Br. licence: 140

Nënshkrimi / Potpis:

Data e rilevimit / Datum snimanja: 13.08.2026

V.V.

Aprovoi / Usvojio:

(emri dhe mbiemri i përsonit zyrtar/ ime i prezime sluzbenog lica)

Nënshkrimi / Potpis:

Data e rilevimit / Datum snimanja:

Zyra kadastrale komunale / Opštinska katastarska kancelarija: Ferizaj

Nr. i njësisë kadastrale / Br. katastarske jedinice : 00492-29

Zona kadastrale / Katastarska zona: Talinoci i Jerlive

Numri i lëndës / Broj predmeta:

Lloji i njësisë kadastrale / Vrsta katastarske jedinice : Ndërtesë

Shkalla e zvoglimit / Razmera plana 1: 500


Republika e Kosovës

Republika Kosova-Republic of Kosova

Qeveria -Vlada-Government

Ministria e Mjedisit dhe Planifikimit Hapësinor /Ministarstvo Sredine i Prostornog Planiranja/Ministry of Environment and Spatial Planning

AGJENCIA KADASTRALE E KOSOVËS/ KATASTARSKA AGECIJA KOSOVA/ KOSOVA CADASTRAL AGENCY

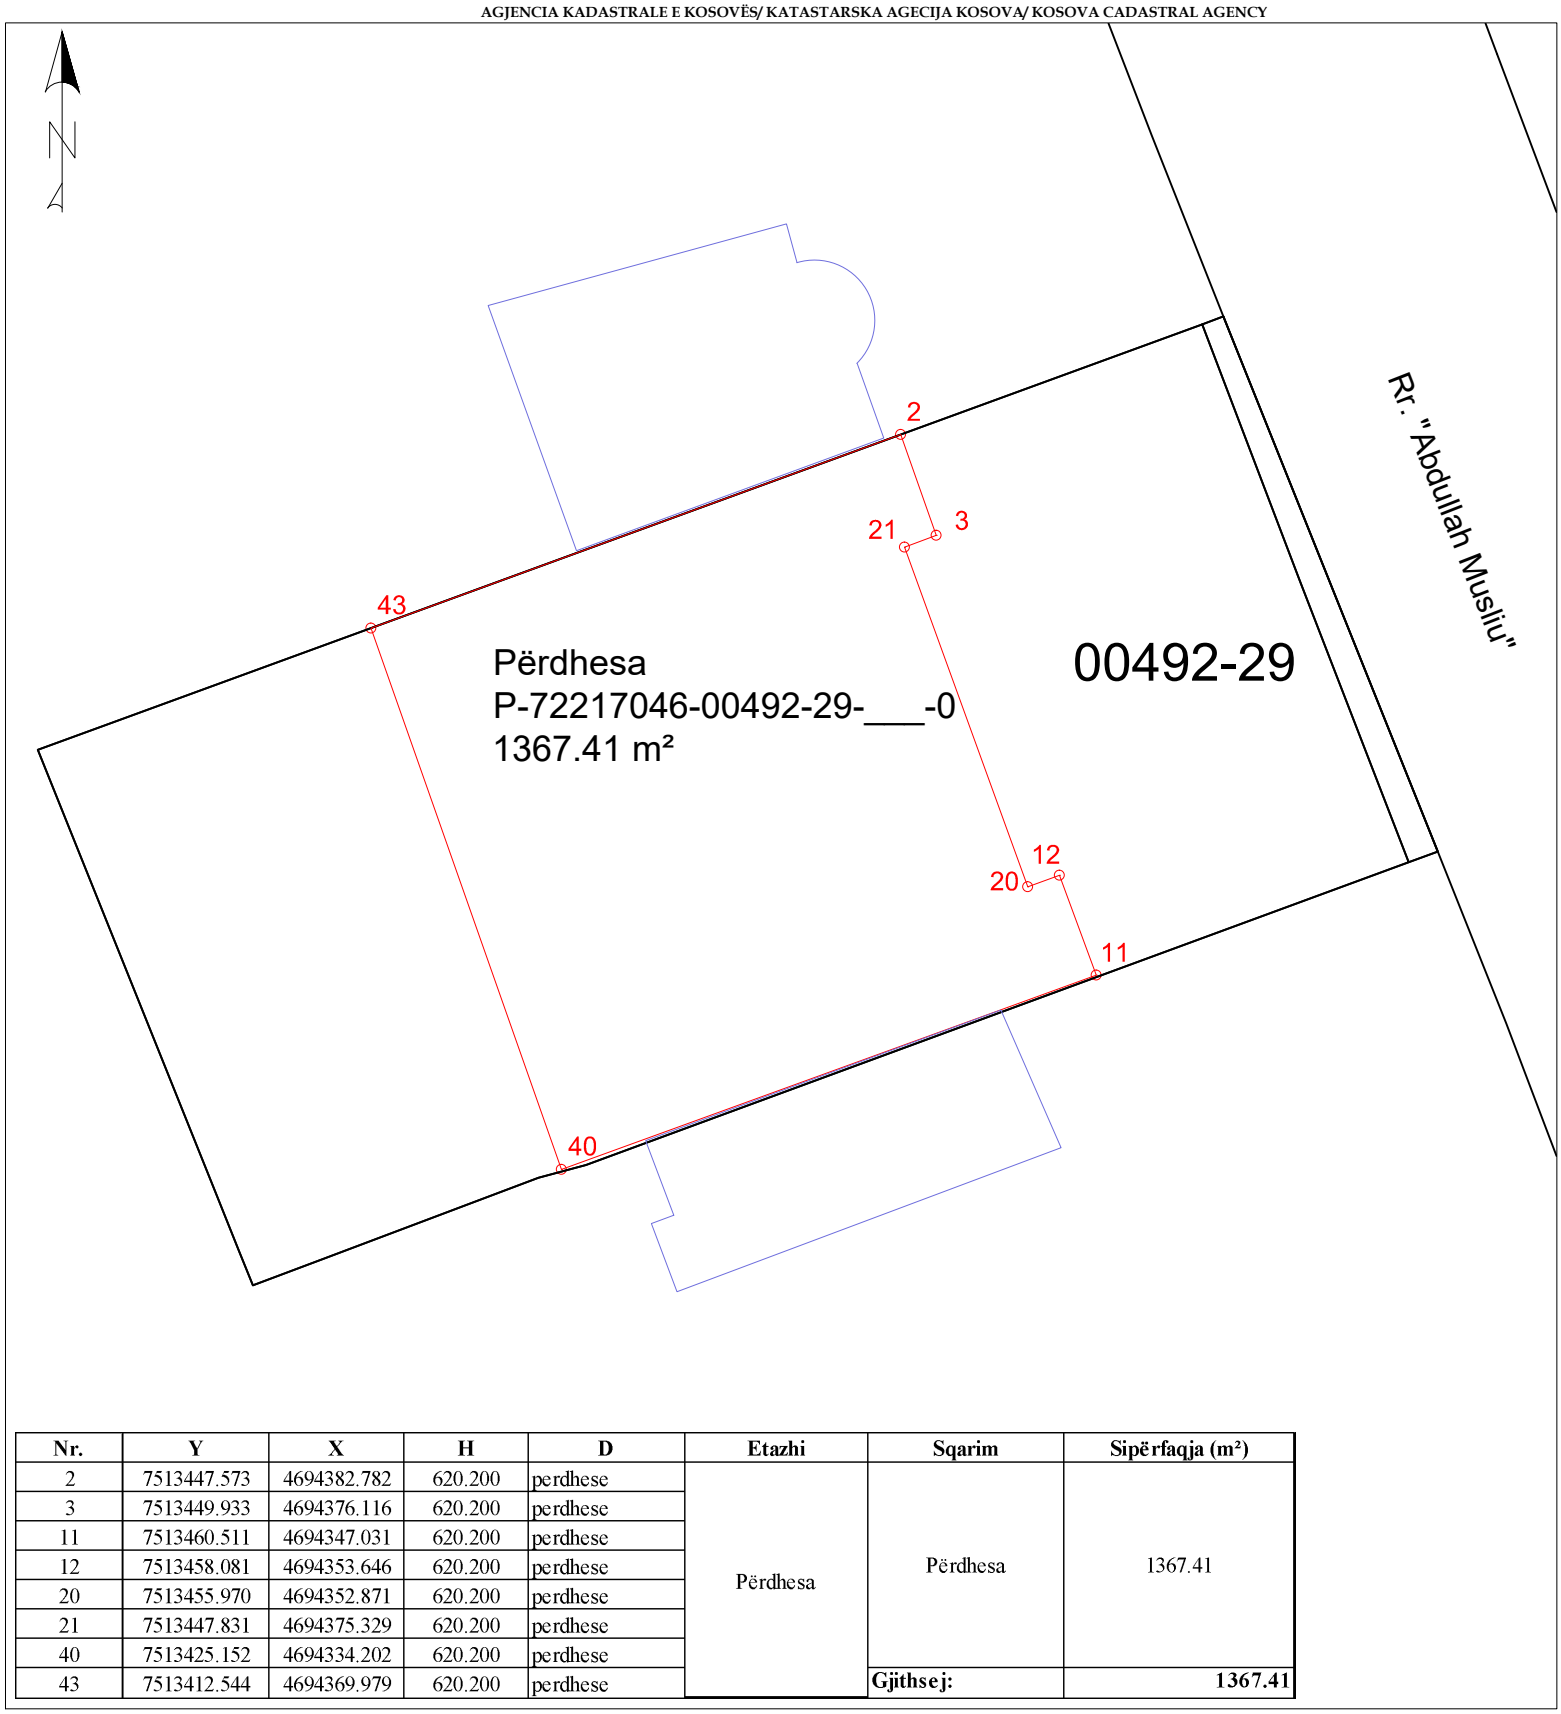

Nr.	Y	X	H	D	Etazhi	Sqarim	Sipërfaqja (m²)
2	7513447.573	4694382.782	620.200	perdhese	Përdhesa	Përdhesa	1367.41
3	7513449.933	4694376.116	620.200	perdhese			
11	7513460.511	4694347.031	620.200	perdhese			
12	7513458.081	4694353.646	620.200	perdhese			
20	7513455.970	4694352.871	620.200	perdhese			
21	7513447.831	4694375.329	620.200	perdhese			
40	7513425.152	4694334.202	620.200	perdhese			
43	7513412.544	4694369.979	620.200	perdhese		**Gjithsej:**	**1367.41**

Rilevoi / Snimio: LIRIDON SEJDIU

(emri dhe mbiemri i gjeodetit/kompanisë/ ime i prezime geodeta/ kompanije)

Nr. i licencës / Br. licence: 140

Nënshkrimi / Potpis:

Data e rilevimit / Datum snimanja: 13.08.2026

V.V.

Aprovoi / Usvojio:

(emri dhe mbiemri i përsonit zyrtar/ ime i prezime sluzbenog lica)

Nënshkrimi / Potpis:

Data e rilevimit / Datum snimanja:

Zyra kadastrale komunale / Opštinska katastarska kancelarija: Ferizaj

Nr. i njësisë kadastrale / Br. katastarske jedinice : 00492-29

Zona kadastrale / Katastarska zona: Talinoci i Jerlive

Numri i lëndës / Broj predmeta:

Lloji i njësisë kadastrale / Vrsta katastarske jedinice : Ndërtesë

Shkalla e zvoglimit / Razmera plana 1: 500


Republika e Kosovës

Republika Kosova-Republic of Kosova

Qeveria -Vlada-Government

Ministria e Mjedisit dhe Planifikimit Hapësinor /Ministarstvo Sredine i Prostornog Planiranja/Ministry of Environment and Spatial Planning

AGJENCIA KADASTRALE E KOSOVËS/ KATASTARSKA AGECIJA KOSOVA/ KOSOVA CADASTRAL AGENCY

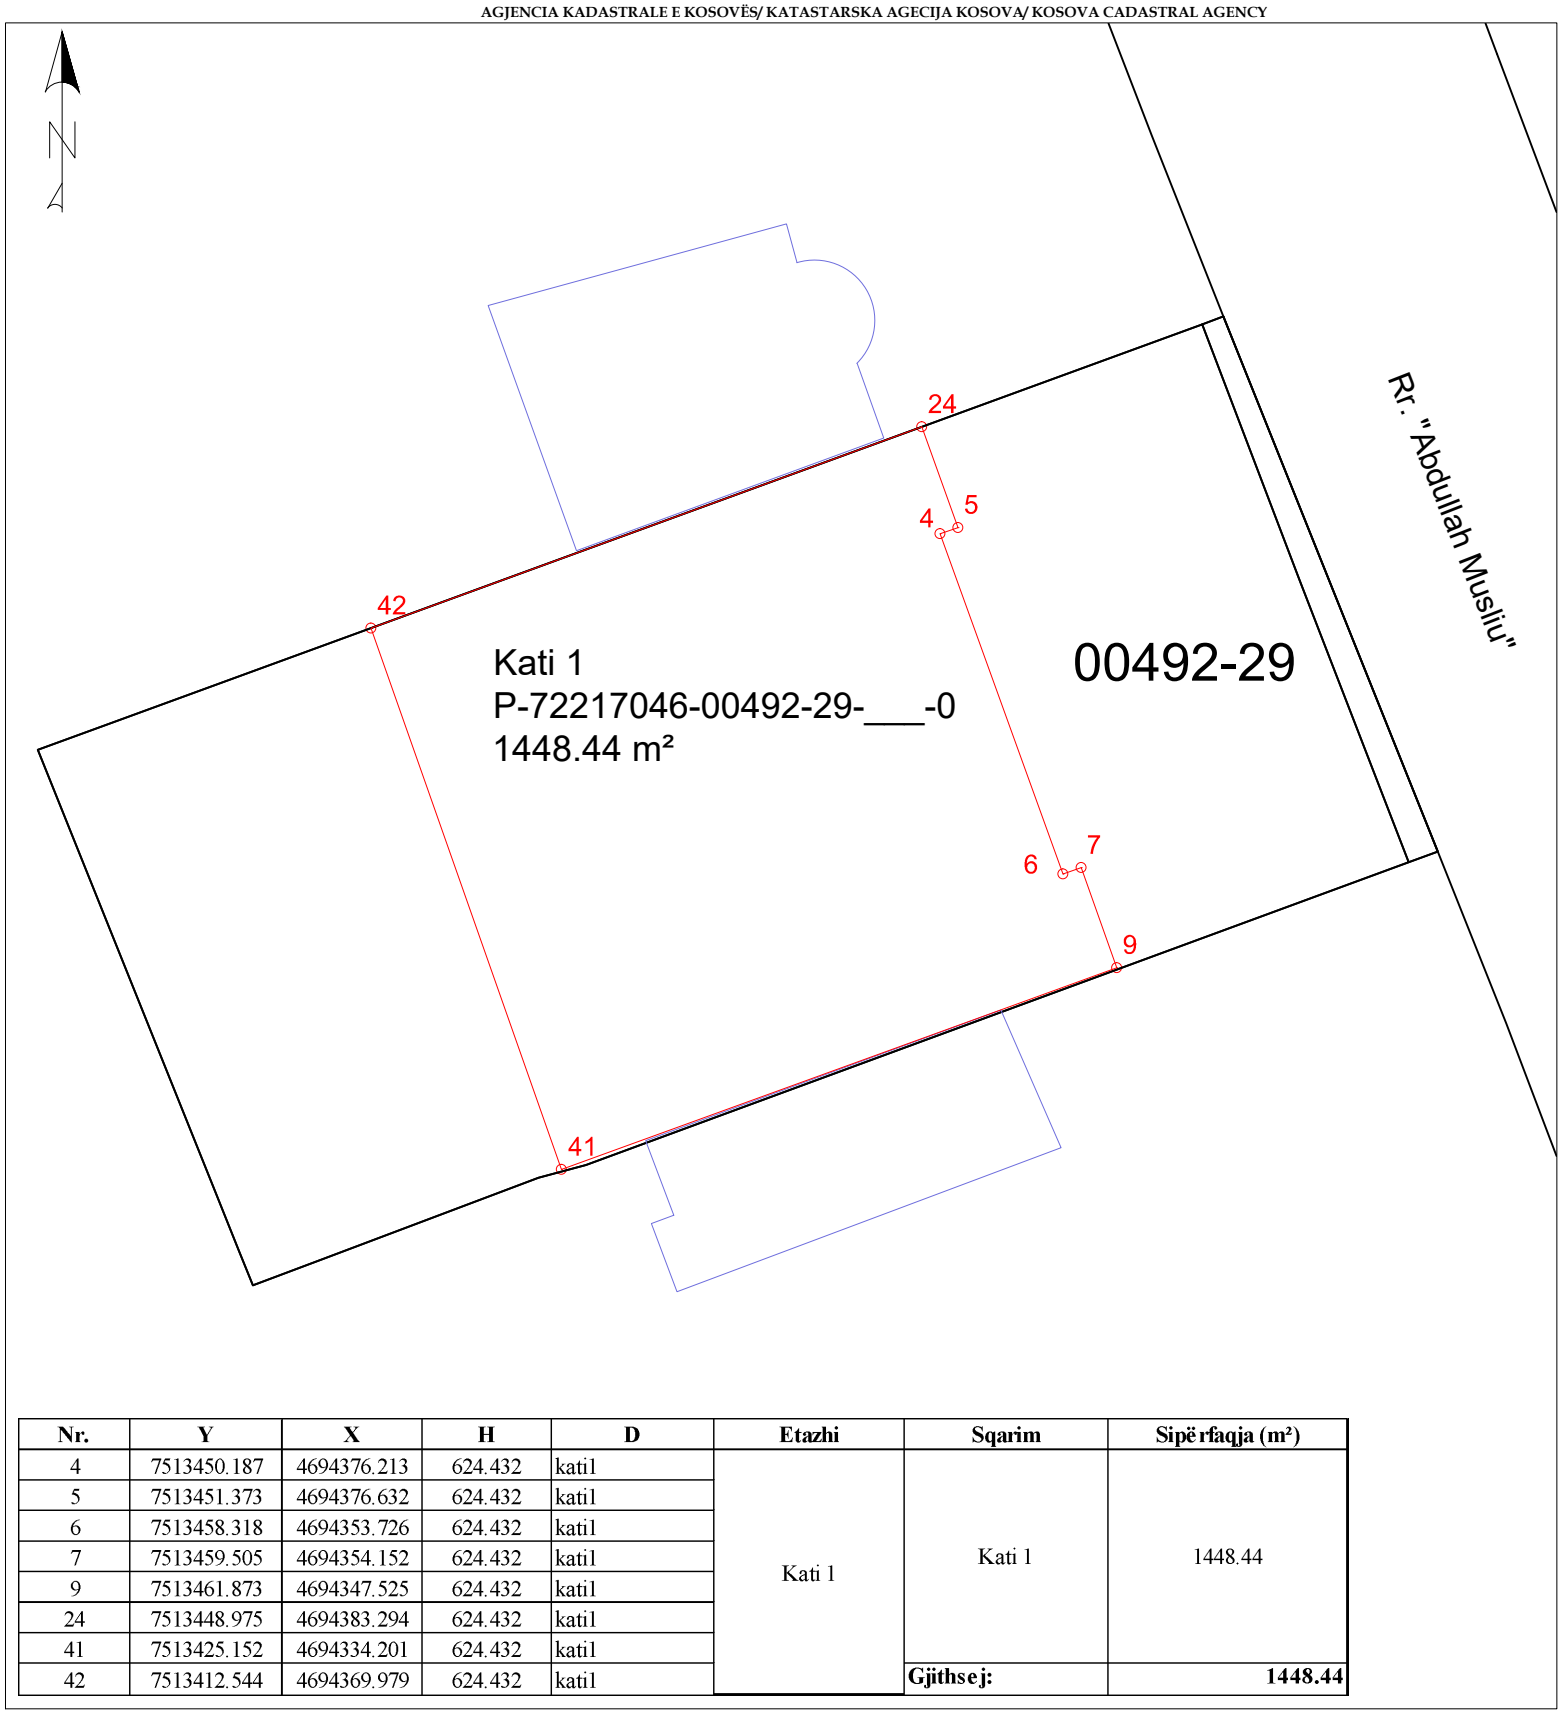

Nr.	Y	X	H	D	Etazhi	Sqarim	Sipërfaqja (m²)
4	7513450.187	4694376.213	624.432	kati1	Kati 1	Kati 1	1448.44
5	7513451.373	4694376.632	624.432	kati1			
6	7513458.318	4694353.726	624.432	kati1			
7	7513459.505	4694354.152	624.432	kati1			
9	7513461.873	4694347.525	624.432	kati1			
24	7513448.975	4694383.294	624.432	kati1			
41	7513425.152	4694334.201	624.432	kati1			
42	7513412.544	4694369.979	624.432	kati1		**Gjithsej:**	**1448.44**

Rilevoi / Snimio: LIRIDON SEJDIU

(emri dhe mbiemri i gjeodetit/kompanisë/ ime i prezime geodeta/ kompanije)

Nr. i licencës / Br. licence: 140

Nënshkrimi / Potpis:

Data e rilevimit / Datum snimanja: 13.08.2026

V.V.

Aprovoi / Usvojio:

(emri dhe mbiemri i përsonit zyrtar/ ime i prezime sluzbenog lica)

Nënshkrimi / Potpis:

Data e rilevimit / Datum snimanja:

Republika e Kosovës
Republika Kosova-Republic of Kosovo
Qeveria e Kosovës- Vlada Kosova- Government of Kosovo
Ministria e Infrastrukturës dhe Ambientit/ Ministrastvo Infrastrukture i Sredine/ Ministry of Infrastructure and Environment
AGJENCIA KADASTRALE E KOSOVËS/KOSOVSKA KATASTARSKA AGENCIJA/ KOSOVO CADASTRAL AGENCY

Komuna: Ferizaj **Zona Kadastrale: Talinoc i Jerlive**
Numri i njësis kadastrale: 00492-29 **Sistemi koordinat: KosovaRef01**

Nr.	Y	X	H	D	Etazhi	Sqarim	Sipërfaqja (m²)
2	7513447.573	4694382.782	620.200	perdhese	Përdhesa	Përdhesa	1367.41
3	7513449.933	4694376.116	620.200	perdhese			
11	7513460.511	4694347.031	620.200	perdhese			
12	7513458.081	4694353.646	620.200	perdhese			
20	7513455.970	4694352.871	620.200	perdhese			
21	7513447.831	4694375.329	620.200	perdhese			
40	7513425.152	4694334.202	620.200	perdhese			
43	7513412.544	4694369.979	620.200	perdhese		**Gjithsej:**	**1367.41**

Nr.	Y	X	H	D	Etazhi	Sqarim	Sipërfaqja (m²)
4	7513450.187	4694376.213	624.432	kati1	Kati 1	Kati 1	1448.44
5	7513451.373	4694376.632	624.432	kati1			
6	7513458.318	4694353.726	624.432	kati1			
7	7513459.505	4694354.152	624.432	kati1			
9	7513461.873	4694347.525	624.432	kati1			
24	7513448.975	4694383.294	624.432	kati1			
41	7513425.152	4694334.201	624.432	kati1			
42	7513412.544	4694369.979	624.432	kati1		**Gjithsej:**	**1448.44**

Nr.	Y	X	H	D	Etazhi	Sqarim	Sipërfaqja (m²)
4	7513444.852	4694381.788	617.000	Bodrumi	Bodrumi	Bodrumi	1312.58
5	7513412.544	4694369.979	617.000	Bodrumi			
6	7513425.152	4694334.202	617.000	Bodrumi			
7	7513457.804	4694346.049	617.000	Bodrumi		**Gjithsej:**	**1312.58**

Gjeodeti / Kompania gjeodete e licencuar:	Liridon Sejdiu	Nënshkrimi dhe vula:	
Numri i licencës	140		

Zyra kadastrale komunale / Opštinska katastarska kancelarija: Ferizaj

Nr. i njësisë kadastrale / Br. katastarske jedinice : 00492-29-___-0

Zona kadastrale / Katastarska zona: Talinoci i Jerlive

Numri i lëndës / Broj predmeta: _____

Lloji i njësisë kadastrale / Vrsta katastarske jedinice : Ndërtesë

Shkalla e zvoglimit / Razmera plana 1: 500


Republika e Kosovës

Republika Kosova-Republic of Kosova

Qeveria -Vlada-Government

Ministria e Mjedisit dhe Planifikimit Hapësinor /Ministarstvo Sredine i Prostornog Planiranja/Ministry of Environment and Spatial Planning

AGJENCIA KADASTRALE E KOSOVËS/ KATASTARSKA AGECIJA KOSOVA/ KOSOVA CADASTRAL AGENCY

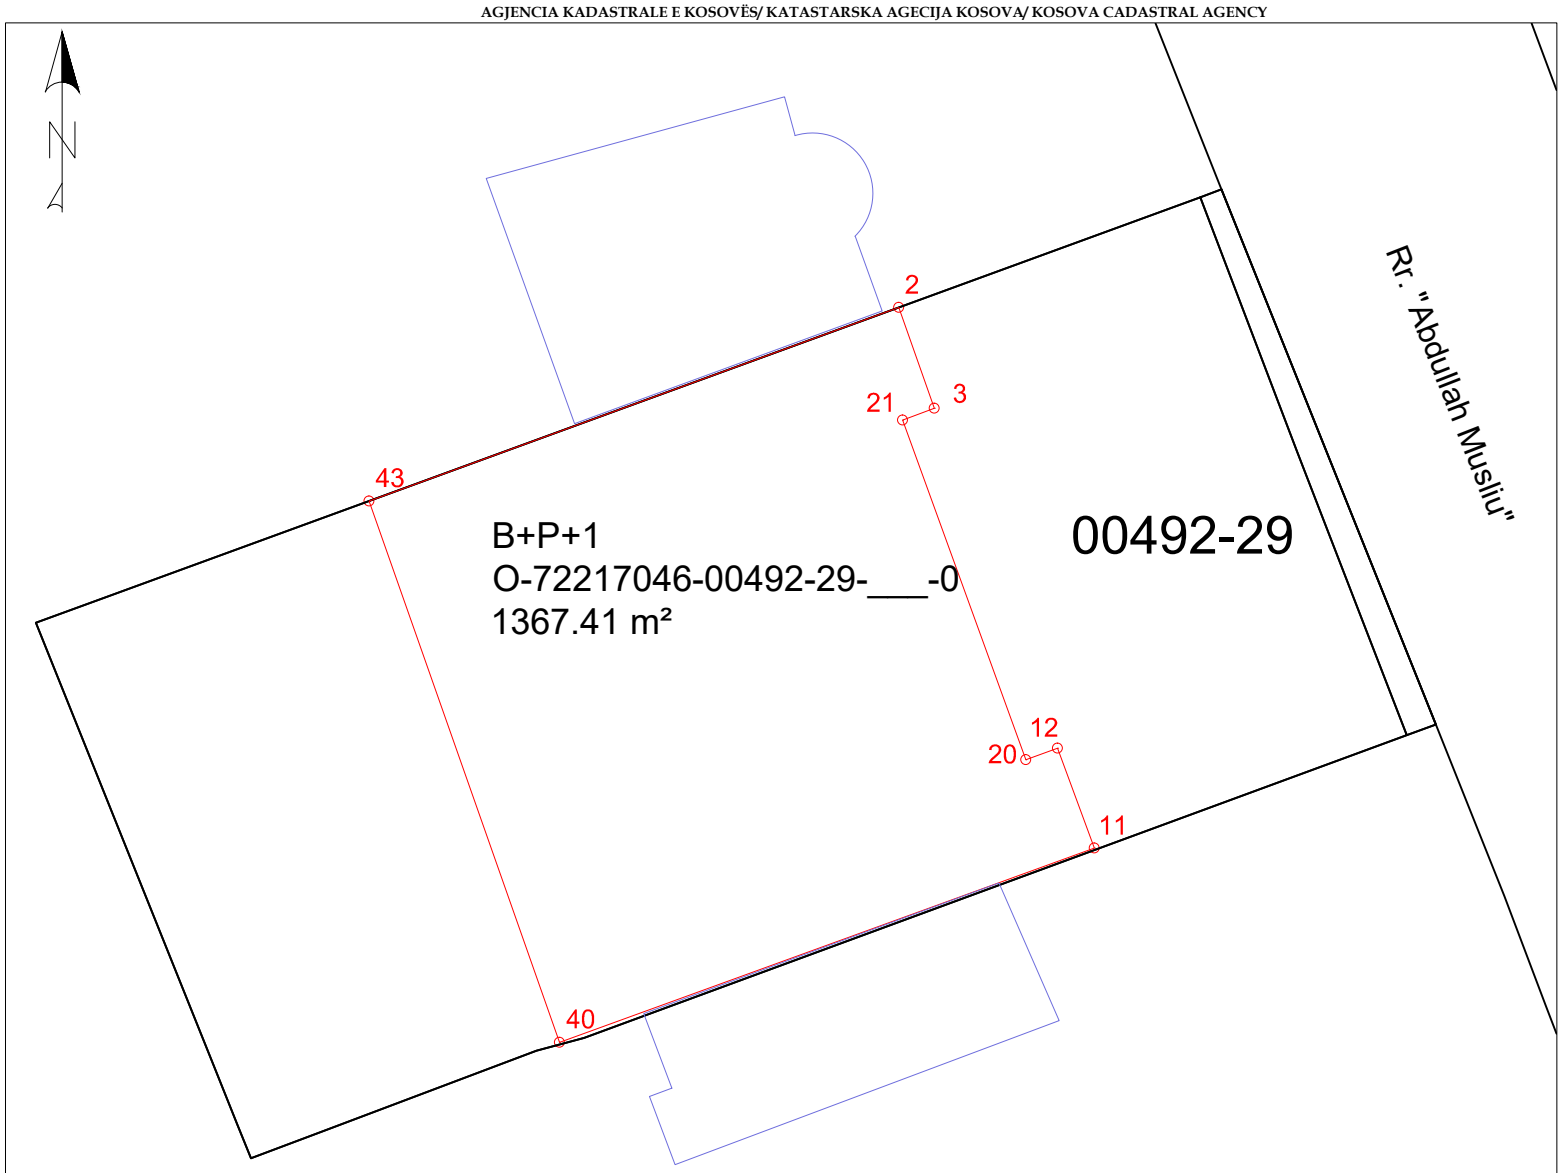

Nr	Y	X	H	Kodi	Përshkrimi	Burimi
2	7513447.573	4694382.782	620.200	40	Shtëpi-Ndërtesë	PM
3	7513449.933	4694376.116	620.200	40	Shtëpi-Ndërtesë	PM
11	7513460.511	4694347.031	620.200	40	Shtëpi-Ndërtesë	PM
12	7513458.081	4694353.646	620.200	40	Shtëpi-Ndërtesë	PM
20	7513455.970	4694352.871	620.200	40	Shtëpi-Ndërtesë	PM
21	7513447.831	4694375.329	620.200	40	Shtëpi-Ndërtesë	PM
40	7513425.152	4694334.202	620.200	40	Shtëpi-Ndërtesë	PM
43	7513412.544	4694369.979	620.200	40	Shtëpi-Ndërtesë	PM

Rilevoi / Snimio: LIRIDON SEJDIU

(emri dhe mbiemri i gjeodetit/kompanisë/ ime i prezime geodeta/ kompanije)

Nr. i licencës / Br. licence: 140

Nënshkrimi / Potpis: _____

Data e rilevimit / Datum snimanja: 13.08.2026

V.V.

Aprovoi / Usvojio: _____

(emri dhe mbiemri i përsonit zyrtar/ ime i prezime sluzbenog lica)

Nënshkrimi / Potpis: _____

Data e rilevimit / Datum snimanja: _____

Republika e Kosovës
Republika Kosova-Republic of Kosovo
Qeveria e Kosovës- Vlada Kosova- Government of Kosovo
Ministria e Infrastrukturës dhe Ambientit/ Ministrastvo Infrastrukture i Sredine/ Ministry of Infrastructure and Environment
AGJENCIA KADASTRALE E KOSOVËS/KOSOVSKA KATASTARSKA AGENCIJA/ KOSOVO CADASTRAL AGENCY

Komuna: Ferizaj	**Zona Kadastrale: Talinoc i Jerlive**
Numri i njësis kadastrale: 00492-29	**Sistemi koordinat: KosovaRef01**

Nr	Y	X	H	Kodi	Përshkrimi	Burimi
2	7513447.573	4694382.782	620.200	40	Shtëpi-Ndërtesë	PM
3	7513449.933	4694376.116	620.200	40	Shtëpi-Ndërtesë	PM
11	7513460.511	4694347.031	620.200	40	Shtëpi-Ndërtesë	PM
12	7513458.081	4694353.646	620.200	40	Shtëpi-Ndërtesë	PM
20	7513455.970	4694352.871	620.200	40	Shtëpi-Ndërtesë	PM
21	7513447.831	4694375.329	620.200	40	Shtëpi-Ndërtesë	PM
40	7513425.152	4694334.202	620.200	40	Shtëpi-Ndërtesë	PM
43	7513412.544	4694369.979	620.200	40	Shtëpi-Ndërtesë	PM

Gjeodeti / Kompania gjeodete e licencuar:	Liridon Sejdiu	Nënshkrimi dhe vula:	
Numri i licencës	140		

Republika e Kosovës
Republika Kosova - Republic of Kosovo
Qeveria e Kosovës - Vlada Kosova - Government of Kosovo
Ministria e Infrastrukturës dhe Ambientit/ Ministrastvo Infrastrukture i Sredine/ Ministry of Infrastructure and Environment
AGJENCIA KADASTRALE E KOSOVËS/ KOSOVSKA KATASTARSKA AGENCIJA/ KOSOVA CADASTRAL AGENCY


R E G J I S T R I M I I NDERTESËS / SHTËPISË

Nr	Komuna	Zona Kadastrale	Numri i ndërtesës (njësia)	Etazhiteti	Katet	Sipërfaqja e kateve [m²]	Sipërfaqja e bazamentit [m²]	Adresa e Njësisë	Vendi i quajtur	Shfrytëzimi i aktual	Pronari / Shfrytëzuesi Emri (Emri i prindit) Mbiemri	Numri përsonal	Pjesa e Pronës
1	Ferizaj	Talinoc I Jerlive	O-72217046-00492-29-___-0	B+P+1	Bodrumi	1312.58	1367.41	Rr. "Abdullah Musliu"	Gropa	Afarizëm	Sylejman (Shefki) Aliu	1004551792	1/1
					Përdhesa	1367.41							
					Kati1	1448.44							
					Gjithsej:	**4128.43**							

Gjeodeti/kompania e licencuar: LIRIDON SEJDIU	Nr i licencës: 140	Nënshkrimi dhe vula:


professional
tools & service
diy & home
MEGAVOLT
KRAUSE


ENSARI 2010
PJESË
KËNETA
MEGA
SJ AA 1918
05 186 DM

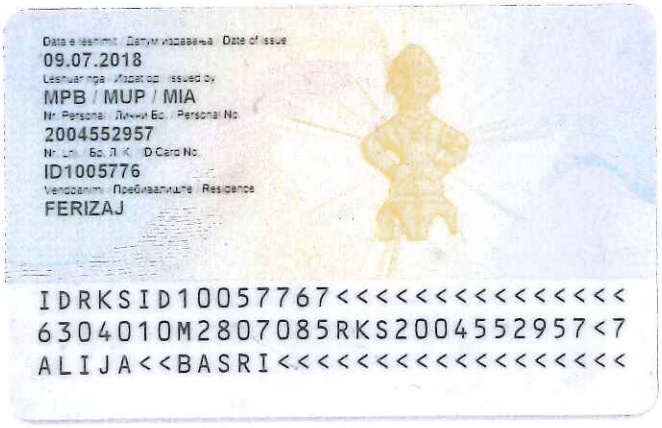
Data e lëshimit / Датум издавања / Date of issue
09.07.2018
Lëshuar nga / Издао / Issued by
MPB / MUP / MIA
Nr. Personal / Лични бр. / Personal No.
2004552957
Nr. Lnr. / Бр. Л.К. / ID Card No.
ID1005776
Vendbanimi / Пребивалиште / Residence
FERIZAJ
IDRKSID10057767<<<<<<<<<<<<<<<
6304010M2807085RKS2004552957<7
ALIJA<<BASRI<<<<<<<<<<<<<<<<<<


REPUBLIKA E KOSOVËS
LETËRNJOFTIM
РЕПУБЛИКА КОСОВО
ЛИЧНА КАРТА
REPUBLIC OF KOSOVO
IDENTITY CARD
Mbiemri / Презиме / Surname
ALIJA
Emri / Име / Given name
BASRI
Datëlindja / Датум рођења / Date of birth
01.04.1963
Gjinia / Пол / Sex
M
Shtetësia / Држављанство / Nationality
KOSOVAR
Data e skadimit / Датум истека / Date of expiry
08.07.2028
Vendlindja / Место рођења / Place of birth
KOMOGLLAVE
Nënshkrimi / Потпис / Signature
ID
177752

Republika e Kosovës
Republika Kosova-Republic of Kosovo
Qeveria - Vlada - Government
Ministria e Mjedisit dhe Planifikimit Hapësinor / Ministarstvo Životne Sredine i Prostornog Planiranja / Ministry of Environment and Spatial Planning
AGJENCIA KADASTRALE E KOSOVËS / KATASTARSKA AGENCIJA KOSOVA / KOSOVO CADASTRAL AGENCY

CERTIFIKATË / CERTIFIKAT / CERTIFICATE

NJËSIA KADASTRALE / KATASTARSKA JEDINICA / CADASTRAL UNIT : P-72217046-00492-29

Numri i lëndës / Broj Predmet / Case Referent Number:	**69441/26**
Data dhe koha e lëshimit / Datum i vreme izdavanja / Date and time of submission:	25.09.2026 - 13:56
Komuna / Opština / Municipality:	FERIZAJ / UROŠEVAC / FERIZAJ
Zona kadastrale / Katastarska Zona / Cadastral Zone:	Talinoci I Jerlive / Talinoci I Jerlive / Talinoci I Jerlive
Zyra Kadastrale Komunale / Opštinska Katastarska Kancelarija / Municipal Cadastral Office:	FERIZAJ / UROŠEVAC / FERIZAJ

A. TË DHËNAT PËR NJËSINË KADASTRALE / PODACI O KATASTARSKOJ JEDINICI / CADASTRAL UNIT DATA

Numri i njësisë kadastrale Broj katastarske jedinice Cad. Unit. No.	Lloji i njësisë Vrsta Jedinice Unit Type	Lloji i pronës Vrsta imovine Property Type	Zona U/R G/S U/R	Sipërfaqja Površina Area (m²)	Përshkrim Opis Description	Krijuar më datën Uradjeno na dan Created On	Azhuruar Ažurirano Updated
P-72217046-00492-29	PARCELË / PARCELA / PARCEL	Pronë private / Privatna Imovina / Privatelly owned Land	Rural	3142	RFP.47/2025	19.09.2025	

A.1 ADRESA E NJËSISË KADASTRALE / ADRESA KATASTARSKE JEDINICE /CADASTRAL UNIT ADDRESS

Vendi i quajtur Mesto zvano Called place	Kodi Postal Poštanski Kod Postal Code	Emri i rrugës Naziv ulice Street name	Krijuar më datën Uradjeno na dan Created On	Azhuruar Ažurirano Updated
GROPA	0		19.09.2025	

REPUBLIKA E KOSOVËS - REPUBLIKA E KOSOVO - KOMUNA FERIZAJ - OPŠTINA UROŠEVAC - FERIZAJ UROŠEVAC

A.2 LLOJI I SHFRYTËZIMIT / VRSTA KORISCENJA / TYPE OF USE

Numri Broj Number	Lloji i shfrytëzimit të parcelës Vrsta koriscenja parcele Parcel Type Of Use	Shfrytëzimi aktual i parcelës Trenutno koriscenje parcele Parcel Current Use	Kualiteti i klasës Kvalitet klase Quality Class	Sipërfaqja (m²) Površina (m²) Area (m²)
1	Bujqësore/Poljoprivredno/Agriculture	Arat/Njive/Arable	Arë E Klasës 3/Njiva 3 Klase/3rd Class Arable Land	**2841**
2	Infrastruktura/Infrastruktura/Infrastructure	Rrugë/Put/Road		**301**

B. PRONARI/POSEDUESI - VLASNIK/DRŽALAC - OWNER/POSSESSOR

Të drejtat Prava Rights	Emri Ime Name	Nr. personal Licni broj ID. No.	Vendbanimi Prebivaliste Resident	Kodi postal Poštanski kod Postal code	Hollësitë e adresës Pojedinosti adrese Address details	Pjesa e pronës Deo imovine Share quota	Pershkrimi Opis Description	Azhuruar Ažurirano Updated
Posedim individual / Individualna Drzavina / Single possessor	**ALIU SYLEJMAN (SHEFKI)**	1004551792	TALINOC I JERLIVE / JERLI TALINOVAC / TALINOFCI I JERLIVE /			**1/1**	63/2011-Bashkimi i ngastrave me kerkesen nr.1572/2011; dt.04.07.2011 RFP.22/2011	23.09.2025

C. HIPOTEKA - HIPOTEKA - MORTGAGE

C.1. Informata për hipotekën - Informacija o hipoteci - Mortgage information

Shuma e borxhit Iznos duga Amount of debt	Shuma e borxhit me shkrim Iznos duga slovima Amount debt in writing	Data e kthimit Datum isteka Due date	Prioriteti Prioritet Priority	Afati dhe kushtet Rokovi i uslovi Terms and conditions	Përshkrim Opis Description	Azhuruar Ažurirano Updated
650000 EUR	GjashtëQindePesëdhjetëMijë	30.06.2032	1	Kontratë për hipotekën LRP.nr./2017, Nr.ref.885/2017	9/2017	23.09.2025

C.2 Komponentët e hipotekës - Komponente hipoteke - Mortgage components

Të drejtat Prava Rights	Emri Ime Name	Nr. personal Licni broj ID. No.	Vendbanimi Prebivalište Residence	Kodi postal Poštanski kod Postal code	Hollësitë e adresës Pojedinosti adrese Address details	Përshkrim Opis Description	Azhuruar Ažurirano Updated
PENGDHËNËSI / Duznik-Hipotekarni / MORTGAGOR	**ALIU SYLEJMAN (SHEFKI)**	1004551792	TALINOC I JERLIVE / JERLI TALINOVAC / TALINOFCI I JERLIVE /			9/2017	23.09.2025
PENGMARRËSI / Poverilac-Hipotekarni / MORTGAGEE	**" PRO CREDIT BANK " Sh.a.**	70050026	PRIZREN / PRIZREN / PRIZREN /		ZAHIR PAJAZITI	9/2017	23.09.2025
BORXHLIU / Duznik / DEBTOR	**" KËNETA " SH.P.K.**	71290476	FERIZAJ / UROŠEVAC / FERIZAJ /		MAGJISTRALJA FERIZAJ-PRISHTINË	9/2017	23.09.2025

REPUBLIKA E KOSOVËS / REPUBLIKA KOSOVA / REPUBLIC OF KOSOVO

QEVERIA E KOSOVËS / VLADA KOSOVA /GOVERNMENT OF KOSOVA

MINISTRIA E MJEDISIT DHE PLANIFIKIMIT HAPËSINOR
MINISTARSTVO ŽIVOTNE SREDINE I PROSTORNOG PLANIRANJA
MINISTRY OF ENVIRONMENT AND SPATIAL PLANNING


AGJENCIA KADASTRALE E KOSOVËS/ KATASTARSKA AGENCIJA KOSOVA/ KOSOVA CADASTRAL AGENCY

KOPJA E PLANIT / KOPIJA PLANA / COPY PLAN

Zyra Kadastrale Komunale/ Opštinska Katastarska Kancelarija /Municipal Cadastral Office : FERIZAJ

Zona Kadastrale / Katastarska Zona / Cadastral Zone: Talinoci i Jerlive

Njësia/Jedinica/Unit	Tipi/Vrsta/Type	Sipërfaqja/Površina/Area m²
P-72217046-00492-29	Parcelë / Parcela / Parcel	3142

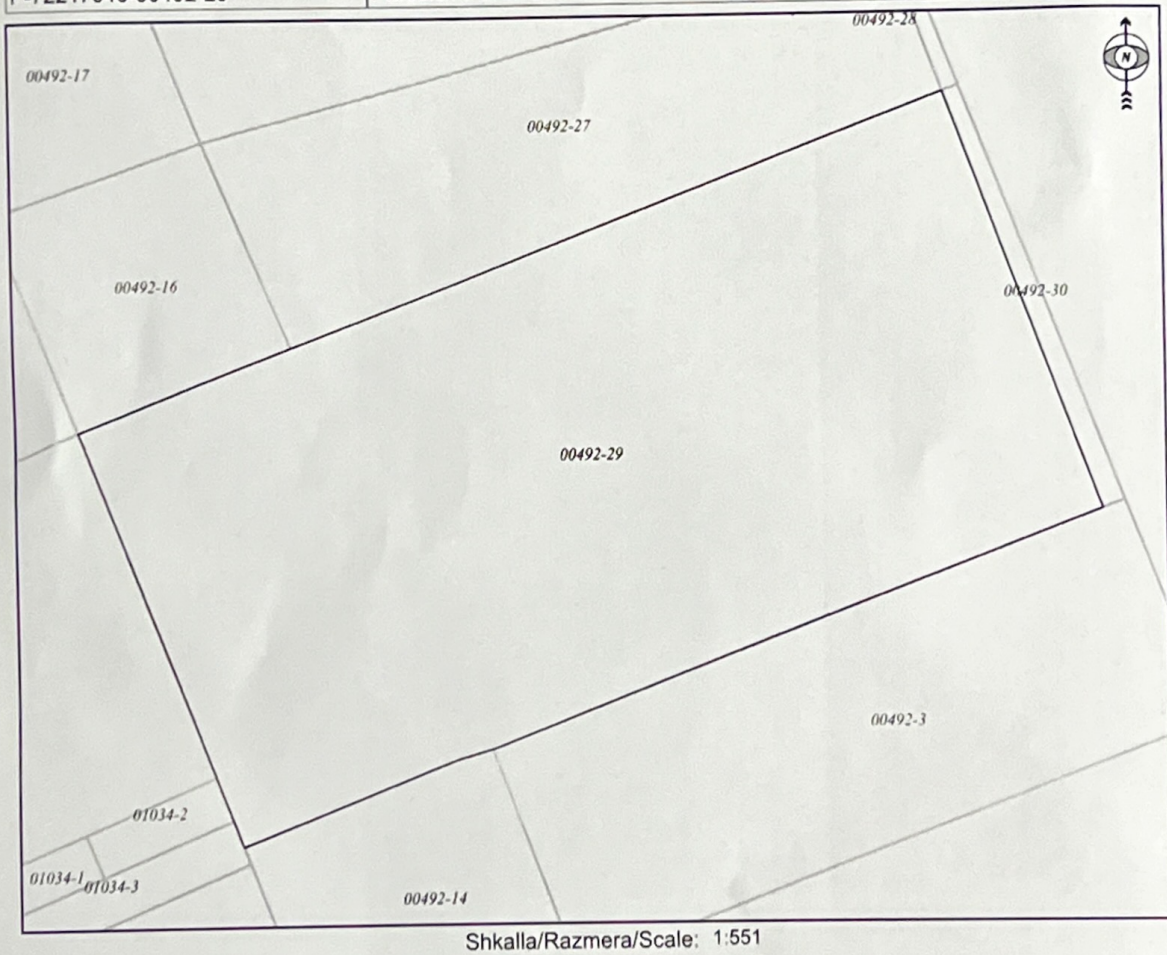

Shkalla/Razmera/Scale: 1:551

Punoi/Obradio/Created: Kimete Hajdini

Nënshkrimi/Potpis/Signature:

Shënim/Beleška/Note:

REPUBLIKA E KOSOVËS - REPUBLIKA KOSOVO
KOMUNA FERIZAJ - OPŠTINA UROŠEVAC
FERIZAJ UROŠEVAC

Data/ Data/Date: 12.11.2026

Koha/ Vreme/ Time: 01:14:18

Republika e Kosovës
Republika Kosova - Republic of Kosovo
Qeveria – Vlada - Government
Ministria e Tregtisë dhe Industrisë - Minstarstvo Trgovine i Industrije
Ministry of Trade and Industry

ARBK
AGJENCIA E REGJISTRIMIT TË BIZNESEVE NË KOSOVË
KOSOVSKA AGENCIJA ZA REGISTRACIJE BIZNISA
KOSOVA BUSINESS REGISTRATION AGENCY

CERTIFIKATË E REGJISTRIMIT
CERTIFIKAT O REGISTRACIJI
CERTIFICATE OF REGISTRATION

810199449

Numri Unik Identifikues / Jedinstveni Matični Broj / Unique Identification Number

KËNETA SH.P.K.

Emri biznesit / Naziv biznisa / Name of business

///

Emri tregtar / Trgovačko ime / Commercial name

Lloji biznesit: Poslovni tip: Business type:	**Shoqëri me përgjegjësi të kufizuara** **Društva sa ograničenom odgovornošću** **Limited Liabilities Companies**
Adresa: Adresa: Address:	**Magjistrale Ferizaj Prishtinë** **Ferizaj**
Data e regjistrimit: Datum registracije: Date of registration:	20/06/2016

15/03/2019
Data / Date / Datum

Nënshkrimi / Signature / Potpis

Nr. ser. / Ser. br. / Ser. No.: **10008572**

Informata mbi biznesin
Information about business
Informacija o biznisu

Numri Unik Identifikues / Jedinstveni Matični Broj / Unique Identification Number
810199449

Aplikacioni / Application / Aplikacija

Subjekti i regjistrimit: **Registration subject:** **Subjekt registracije:**	
Data e plotësimit: **Filling date:** **Datum:**	20/06/2016
Data e pranimit: **Reception date:** **Datum primljenje:**	20/06/2016
Numri i protokollit: **Protocol number:** **Broj protokola:**	0A0000332

Biznesi / Business/ Biznis

Tipi i biznesit **Business Type** **Tip biznisa**	Shoqëri me përgjegjësi të kufizuara Limited Liabilities Companies Društvo sa ograničenom odgovornošću
Emri i biznesit: **Business name:** **Naziv biznisa:**	KËNETA SH.P.K.
Emri tregtar: **Trgovačko ime:** **Commercial name:**	///
Adresa **Address** **Adresa**	Magjistrale Ferizaj Prishtinë Ferizaj
Data e themelimit: **Date of establishment:** **Datum osnivanja:**	20/06/2016
Kapitali i përgjithshëm: **Total Capital:** **Totaini kapital:**	€ 1,200,000.00
Numri i punëtorëve: **Number of employees:** **Broj radnika:**	8

Informata mbi biznesin
Information about business
Informacija o biznisu

Numri Unik Identifikues / Jedinstveni Matični Broj / Unique Identification Number
810199449

Shënim me rëndësi / Important Note / Vazan podatak

; Numri mëparshëm i biznesit është NRB: 71290476 , me zbatimin e ligjit për numrin unik te identifikues te biznesit ka ketë numër NUI: 810199449

Informata plotësuese / Additional Information Note / Dodatna informacija

Informata mbi biznesin
Information about business
Informacija o biznisu

Numri Unik Identifikues / Jedinstveni Matični Broj / Unique Identification Number
810199449

Veprimtaritë / Activities / Delatnosti

4662	Aktiviteti kryesor i biznesit	Tregtia me shumicë e veglave të makinerive Wholesale of machine tools rgovina na veliko alatnim mašinama
4690	Aktiviteti sekondar	Tregtia me shumicë jo e specializuar Non-specialised wholesale trade Nespecijalizirana trgovina na veliko
4799	Aktivitetet tjera	Tregtia tjetër me pakicë, jo në dyqane, tezga ose tregje Other retail sale not in stores, stalls or markets Ostala maloprodaja ne u prodavnicama,tezge ili pijace
4671	Aktivitetet tjera	Tregtia me shumicë e lëndëve djegëse të ngurta, të lëngëta ose të gazta dhe produkteve të lidhur me to Wholesale of solid, liquid and gaseous fuels and related products Trgovina na veliko krutim, tekućim i plinovitim gorivima i srodnim proizvodima
4674	Aktivitetet tjera	Tregtia me shumicë e pjesëve elektronike, pajisjeve hidraulike dhe të ngrohjes, si dhe pjesëve të furnizimit Wholesale of hardware, plumbing and heating equipment and supplies Trgovina na veliko željeznom robom, instalacijskim materijalom i opremom za vodovod i grejanje
4675	Aktivitetet tjera	Tregtia me shumicë e produkteve kimike Wholesale of chemical products Trgovina na veliko hemijskim proizvodima
4618	Aktivitetet tjera	Aktivitetet e ndërmjetësimit të specializuar për shitjen e produkteve të veçanta Agents specialised in the sale of other particular products Posredovanje u trgovini specijaliziranoj za određene proizvode
4622	Aktivitetet tjera	Tregtia me shumicë e luleve dhe bimëve Wholesale of flowers and plants Trgovina na veliko cvećem i sadnicama
4642	Aktivitetet tjera	Tregtia me shumicë e veshjeve dhe këpucëve Wholesale of clothing and footwear Trgovina na veliko odjećom i obućom
4643	Aktivitetet tjera	Tregtia me shumicë e pajisjeve elektroshtëpiake Wholesale of electrical household appliances Trgovina na veliko električnim aparatima za domaćinstvo
4647	Aktivitetet tjera	Tregtia me shumicë e mobilieve, qilimave dhe pajisjeve të ndriçimit Wholesale of furniture, carpets and lighting equipment Trgovina na veliko nameštajem, sagovima i opremom za rasvetu

Informata mbi biznesin
Information about business
Informacija o biznisu

4649	Aktivitetet tjera	Tregtia me shumicë e artikujve të tjerë shtëpiakë Wholesale of other household goods Trgovina na veliko ostalim proizvodima za domaćinstvo
4661	Aktivitetet tjera	Tregtia me shumicë e makinerive bujqësore, pajisjeve dhe pjesëve furnizuese Wholesale of agricultural machinery, equipment and supplies Trgovina na veliko poljoprivrednim mašinama, opremom i priborom

Filialet / Branches / Jedince

Bordi drejtorëve / Board of Directors / Upravni odbor

Pronarët / Owners / Vlasnici

Person fizik

Emri: **Name:** **Ime:**	Basri Alija
ID Personale: **Personal ID:** **Licni ID:**	2004552957
Adresa: **Address:** **Adresa:**	Rr.Rexhep Bislimi Pn. Ferizaj, Kosova
Përgjegjësia: **Liability:** **Odgovornost:**	
Pjesa në pronë: **Owned part:** **Deo o vlasnistvu:**	600,000.00€
Data lindjes: **Birthdate:** **Datum rođenja:**	01/04/1963

[X] Aksionar / Shareholder / Akcionarsko

[ ] Aksionar i privilegjuar / Privileged shareholder/ Privilegovani akcionar

Informata mbi biznesin
Information about business
Informacija o biznisu

Person fizik

Emri: **Name:** **Ime:**	Hyzri Aliu
ID Personale: **Personal ID:** **Licni ID:**	1012165087
Adresa: **Address:** **Adresa:**	Rr " Sali Çeku " Banesë Kati.1 , Nr.107 Ferizaj, Kosova
Përgjegjësia: **Liability:** **Odgovornost:**	
Pjesa në pronë: **Owned part:** **Deo o vlasnistvu:**	600,000.00€
Data lindjes: **Birthdate:** **Datum rođenja:**	20/11/1969

[X] Aksionar / Shareholder / Akcionarsko

[ ] Aksionar i privilegjuar / Privileged shareholder/ Privilegovani akcionar

Personat e autorizuar / Authorized participants / Ovlascene lice

Emri: **Name:** **Ime:**	Hyzri Aliu
ID Personale: **Personal ID:** **Licni ID:**	1012169087
Pozita e punës: **Job position:** **Radno mesto:**	Drejtor dhe Agjent i Regjistruar
Adresa: **Address:** **Adresa:**	Magjistrale - Ferizaj - Prishtinë Ferizaj, Kosova
Autorizimet: **Authorizations:** **Autorizacije:**	